МНОГОКВАРТИРНЫЙ ЖИЛОЙ КОМПЛЕКС
РАСПОЛОЖЕННЫЙ: г. ПЕТРОПАВЛОВСК ул. Ш. Валиханова 9

ПРОЕКТИРОВЩИК: ТОО «LEVEX» ДИРЕКТОР Доскулов Д. Б. МНС №0000133 АСТАНА 2023г.

СОГЛАСОВАНО: ГУ «УПРАВЛЕНИЕ АРХИТЕКТУРЫ, ГРАДОСТРОИТЕЛЬСТВА И ЗЕМЕЛЬНЫХ ОТНОШЕНИЙ г. ПЕТРОПАВЛОВСК»_____

ЗАКАЗЧИК: _____ТОО «ОНДАСЫН СТРОЙ»

ОБЩИЕ УКАЗАНИЯ

Проект разработан на основании постановления АПЗ № и задания заказчика.

В соответствии с архитектурно-планировочным заданием на проектирование.

Рабочий проект разработан для строительства в 1В климатическом подрайоне с расчетной зимней температурой наружного воздуха - 34,8°

Вес снегового покрова	- 1.0 кПа
Скоростной напор ветра	- 0.6 кПа

ХАРАКТЕРИСТИКА ЗДАНИЯ

Класс по функциональной пожарной опасности	- Ф 1.3
Уровень ответственности	- II-нормальный
Степень огнестойкости	- II
Степень долговечности здания	- II
Класс комфортности	- IV

АРХИТЕКТУРНО-ПЛАНИРОВОЧНОЕ РЕШЕНИЕ

"Многоквартирный жилой комплекс , расположенный в г. Петропавловск, ул. Ш. Валиханова 9, представляет собой объемно-пространственной композиции жилого комплекса, состоящего из 9-ти этажных жилых блоков, с внутренним дворовым пространством .

Архитектурные решения воплотились в простых и ясных формах, соразмерных с масштабом городской застройки, выражающих четкий шаг и ясный ритм элементов фасада. Жилые блоки здания соответствует функциональному назначению и имеет современный силуэт с учетом унификации строительных элементов и конструкций, а также градостроительной значимости объекта. Навесной вентилируемый фасад из HPL панелей , керамический облицовочный кирпич, минераловатный утеплитель НГ согласно теплотехническому расчету.

Во внутреннем дворовом пространстве расположены спортивные площадки, детские площадки, площадки для отдыха взрослых, элементы озеленения и ландшафта.

В подвале располагаются подвальные и технические помещения.

На 1-м этаже Жилого комплекса распологаются , тамбур, лифтовые холлы, коридоры, встроенные помещения и квартиры. Входы в встроенные помещения осуществляются с внешней стороны (с прилегающих улиц), в квартиры с внутреннего дворового пространства.

В проекте предусмотрено остекление балконов и лоджий.

Вертикальная коммуникация в здании обеспечивается с помощью лестничной клетки типа Н1, а также , пассажирским лифтом грузоподъемностью 1000 кг.

За отметку 0,000 взят уровень чистого пола первого этажа.

Высота 1-го этажа 3.00м. от пола до потолка, высота 2-го до 9-го этажей 3,0м. от пола до потолка.

В здании предусмотрены следующие виды инженерного оборудования: централизованное отопление, горячее водоснабжение, водопровод, канализация, электроосвещение, телефонизация, пожарная сигнализация.

В проекте предусмотрены мероприятия для маломобильных групп населения согласно

СП РК 3.06-101-2012 «Проектирование зданий и сооружений с учетом доступности для маломобильных групп населения.»:

- С планировочной отметки земли (тротуара) к входам в здание предусмотрены крыльца, с перепадом высот в 7 ступеней. Данный крыльца оборудованы подъемниками , расположены вдоль всего здания и обеспечивают доступность к встроенным помещениям и к подъездам жилой части здания расположенных на 1-ом этаже, на отметке 0.000. .

БЛАГОУСТРОЙСТВО ТЕРРИТОРИИ:

- асфальтобетонные проезды и автостоянки:
- пешеходные тротуары и площадки с покрытием из цементно - песчаной брусчатки;
- озеленение газоны, цветники, деревья;
- площадка для отдыха взрослых;
- площадка для детей;
- спортивная площадка;
- хозяйственная площадка;
- площадка для ТБО.

КОНСТРУКТИВНОЕ РЕШЕНИЕ

Фундаменты – свайные с монолитным железобетонным ростверком по расчету.
Конструктивная схема – бескаркасная.
Наружные стены ниже отм. 0.000 – монолитные железобетонные, толщина- по расчету.
Наружные стены выше отм. 0.000 - кирпичная армированная кладка, толщина по расчету, кирпич керамический полнотелый марки КР-р-по 250х120х88/1,4НФ/150/2,0/50 ГОСТ 530-2012 на цементно-песчаном растворе М 75;
Внутренние стены – кирпичная армированная кладка, толщина по расчету, кирпич керамический полнотелый марки КР-р-по 250х120х88/1,4НФ/150/2,0/50 ГОСТ 530-2012 на цементно-песчаном растворе М 50.
Общие перегородки – кирпич керамический полнотелый марки КР-р-по 250х120х88/1,4НФ/150/2,0/50 ГОСТ 530-2012 толщ 120 мм
Межквартирные перегородки – кладка толщиной 250 мм (блоки из ячеистых бетонов 100 мм - минплита 50 мм - блоки из ячеистых бетонов 100 мм). В местах установки дверей входов квартиры выполнить часть стен выполнить кладкой из керамического кирпича толщиной 250мм на цементно-песчаном растворе М 50.
В качестве шумоизоляции межквартирных стен принять минераловатные плиты «Knauf Акустика» толщиной 50мм (или аналог).
Межкомнатные перегородки, санузлы - кирпич керамический полнотелый марки КР-р-по 250х120х88/1,4НФ/150/2,0/50 ГОСТ 530-2012 толщ 120 мм на цементно-песчаном растворе М50.
Перемычки – железобетонные брусковые по серии 1.038.1-1 вып.1 и индивидуальные.
Ограждение инженерных коммуникаций в квартирах – обшивка гипсокартонными системами по действующим сериям с двумя слоями листов ГКЛВ.
Ограждение инженерных коммуникаций в общем коридоре – из газоблока 100 мм на кладочно-клеевой сухой смеси.
Утепление входных тамбуров и внутри лоджий – минераловатный утеплитель НГ с толщиной согласно теплотехническому расчету с последующим оштукатуриванием по синтетической сетке.
Перекрытия и покрытие - сборные ж/б плиты.
Лестницы – сборные монолитные ж/б марши шириной 1200мм.
Лифты – грузопассажирский лифт грузоподъёмностью 1000кг без машинного помещения. Кабина лифта должна иметь внутренние размеры 2,10 х 1,30 м. Предел огнестойкости дверей шахт лифтов принять не менее EI30.
Кровля – неэксплуатируемая малоуклонная бесчердачная рулонная совмещенная вентилируемая с организованным внутренним водостоком. Минераловатный утеплитель НГ в составе покрытия с толщиной согласно теплотехническому расчету.
Покрытие кровли - трехслойный ковер ТЕХНОЭЛАСТ (ЭКП, ЭПП). Верхний слой - ЭКП с крупнозернистой посыпкой.
Двери входные наружные, тамбурные – алюминиевые остекленные. Двери входов в подъезды оборудовать видеодомофонами и доводчиками. Высота входных дверей 2.4 м с заполнением стеклопакетами из закаленного стекла Двери входов в подвал-стальные,высотой не более 2,1м

ВЕДОМОСТЬ ЧЕРТЕЖЕЙ

№ п.п	Наименование	Примечания
1	ОБЩИЕ ДАННЫЕ. ВЕДОМОСТЬ ЧЕРТЕЖЕЙ.	
2	ТЭП	
3	СИТУАЦИОННАЯ СХЕМА М1:2000	
4	ГЕНЕРАЛЬНЫЙ ПЛАН М1:500	
5-8	ВИДОВАЯ КАРТИНКА	
9	НОЧНАЯ ПОДСВЕТКА	
10	ФАСАДЫ В ОСЯХ 1-4;А-Г;4-1;Г-А	
11	ВЕДОМОСТЬ НАРУЖНЕЙ ОТДЕЛКИ	
12	СЕКЦИЯ 1 ПЛАН ПОДВАЛА	
13	СЕКЦИЯ 2 ПЛАН ПОДВАЛА	
14	СЕКЦИЯ 3 ПЛАН ПОДВАЛА	
15	СЕКЦИЯ 1 ПЛАН 1-ГО ЭТАЖА	
16	СЕКЦИЯ 2 ПЛАН 1-ГО ЭТАЖА	
17	СЕКЦИЯ 3 ПЛАН 1-ГО ЭТАЖА	
18	СЕКЦИЯ 1 ПЛАН ТИПОВОГО ЭТАЖА	
19	СЕКЦИЯ 2 ПЛАН ТИПОВОГО ЭТАЖА	
20	СЕКЦИЯ 3 ПЛАН ТИПОВОГО ЭТАЖА	
21	СЕКЦИЯ 1 ПЛАН КРОВЛИ	
22	СЕКЦИЯ 2 ПЛАН КРОВЛИ	
23	СЕКЦИЯ 3 ПЛАН КРОВЛИ	
24	СЕКЦИЯ 1 РАЗРЕЗ 1-1	
25	СЕКЦИЯ 2 РАЗРЕЗ 1-1	
26	МАЛЫЕ АРХИТЕКТУРНЫЕ ФОРМЫ	

				МНОГОКВАРТИРНЫЙ ЖИЛОЙ КОМПЛЕКС РАСПОЛОЖЕННЫЙ г. ПЕТРОПАВЛОВСК ул. Ш. Валиханова 9	Стадия	Лист	Листов
					ЭП	1	26
				ВЕДОМОСТЬ ЧЕРТЕЖЕЙ. ОБЩИЕ ДАННЫЕ.	ТОО «LEVEX»		
Выполнил	Терехов А.		06.23				

СХЕМА БЛОКИРОВКИ

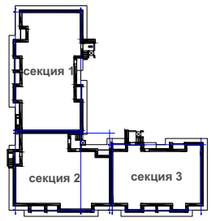

ТЕХНИКО - ЭКОНОМИЧЕСКИЕ ПОКАЗАТЕЛИ

	Наименование	единиц изм.	Количество	Примечание
	Площадь участка	*га.*	**0,4712**	
	Этажность комплекса	*эт.*	**9**	
	Площадь застройки комплекса	*кв.м.*	**1285,2**	
	Общая площадь жилого комплекса	*кв.м*	**8 676,1**	
	Общая площадь квартир	*кв.м.*	*6 676,78*	
	Общая площадь ВП	*кв.м.*	*42,02*	
	Площадь помещений общего пользования	*кв.м.*	*810,47*	
	Общая площадь тех. помещений	*кв.м.*	*1 146,83*	
	Строительный объем комплекса	*кв.м*	**37 994,3**	
	Количество квартир	*куб.м.*	**115**	
	1-комн.	*шт.*	*45*	
	2-комн.	*шт.*	*51*	
	3-комн.	*шт.*	*19*	
	.			
	Количество парковочных мест			
	В границе участка	*шт.*	*22*	
	Площадь озеленения	*кв.м.*	**978,10**	
	Класс жилья	*класс*	**IV**	
	Жилая площадь	*кв.м*	**3 448,11**	

РАСЧЕТ ОБЕСПЕЧЕННОСТИ ПАКОВОЧНЫМИ МЕСТАМИ ПО ОБЪЕКТУ

Класс жилья	**IV**	
Жилая площадь комплекса	**3 448,11**	**кв.м**
Этажность комплекса	**9**	
Количество жителей	**230**	
(согласно п. 6.0.2 СНиП РК 3.01-01 Ас-2007 и Таблица 1 СП РК 3.02-101-2012 - 15 м2		
жилой площади на 1 человека)		
Общая площадь ВП	**42,02**	**кв. м**

Расчет потребности в парковочных местах для жильцов

(согласно СП РК 3.02-101-2012 Таблица 1*):

Комнатность квартир	Кол-во квартир	Коэф. для IV класса жилья	Кол-во м/мест
1-комнат.	45	0,5	22
2-комнат.	51	0,5	25
3-комнат.	19	0,5	9
Всего требуется машиномест для жильцов			**56**

Расчет потребности в гостевых парковочных местах

(согласно п. 4.4.7.5 СП РК 3.02-101-2012) :

Кол-во жителей	Кол-во м/м на 1 000 жителей	Итого
230	100	23
Всего требуется машиномест для гостевого посещениия		**23**

Расчет потребности в парковочных местах для встроенных помещений

(согласно таблицы 13.26 СНиП РК 3.01-01Ас-2007):

Общая площадь ВП	Кол-во расчетных единиц на м2	Итого
42,02	70	1
Всего требуется машиномест для ВП		**1**
ИТОГО ТРЕБУЕТСЯ ПАРКОВОЧНЫХ МЕСТ ПО РАСЧЕТУ		**80**
ОБЩЕЕ КОЛИЧЕТВО ПАРКОВОЧНЫХ МЕСТ ПО ПРОЕКТУ		**30**

ВНИМАНИЕ!!!
Площади помещений и технико-экономические показатели подсчитаны предварительно. Планировка и размеры помещений будут откорректированы и уточнены в рабочем проекте с учетом требований инженерных разделов. Указанные на планах площади не являются основанием для продажи.

				МНОГОКВАРТИРНЫЙ ЖИЛОЙ КОМПЛЕКС РАСПОЛОЖЕННЫЙ г. ПЕТРОПАВЛОВСК ул. Ш. Валиханова 9	Стадия	Лист	Листов
					ЭП	3	26
				СИТУАЦИОННАЯ СХЕМА М1:2000	ТОО «LEVEX»		
Выполнил	Терехов А.		06.23				

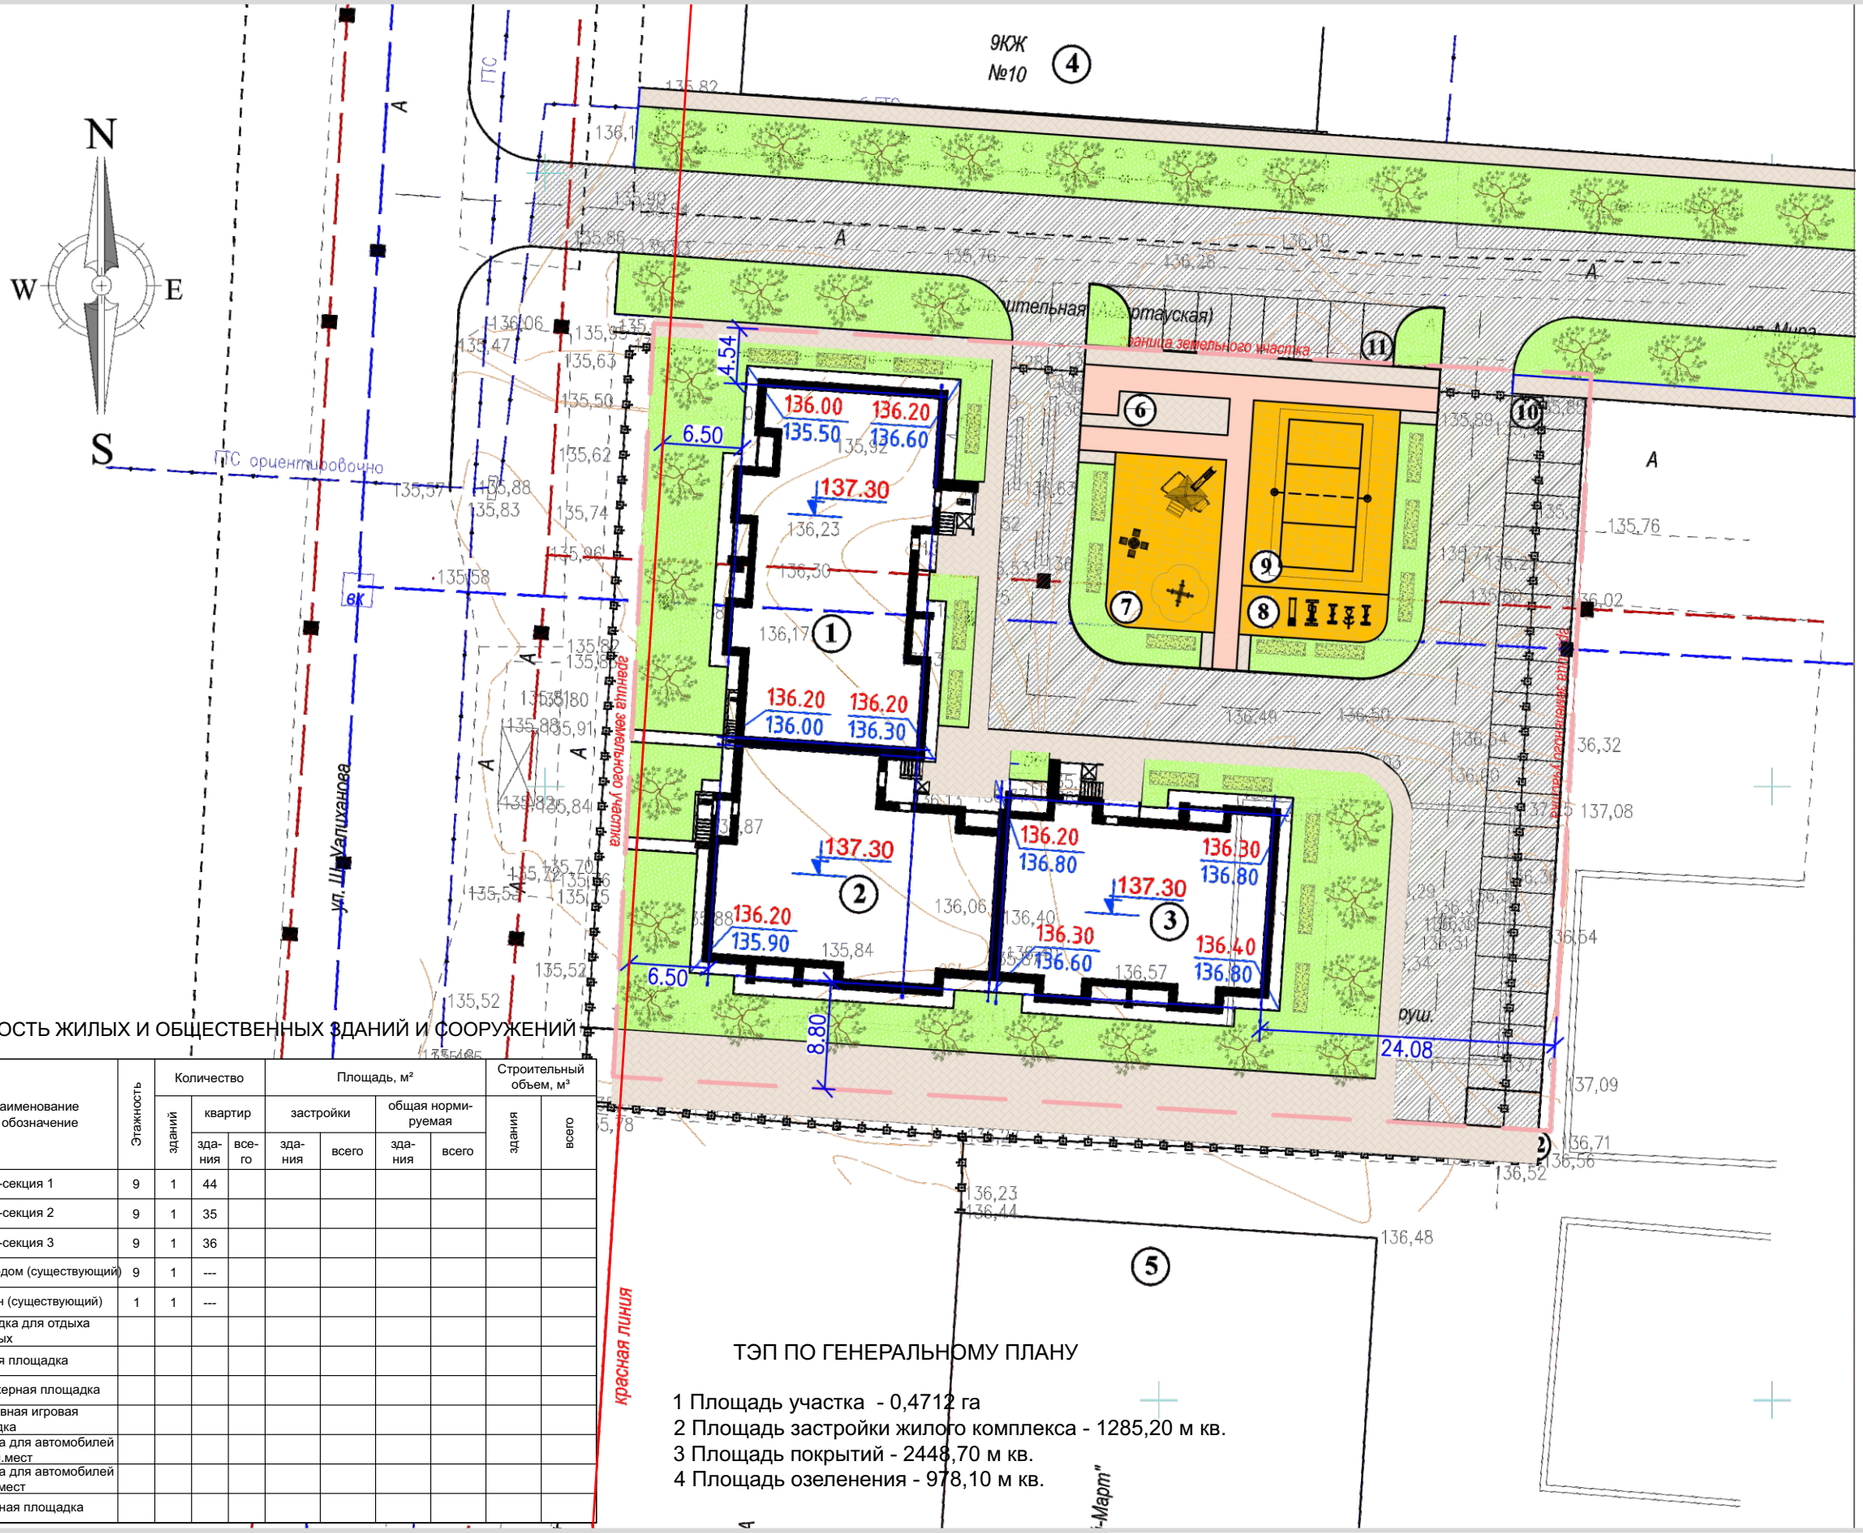
N
W
E
S
9КЖ
№10
4
ГПС
ГПС ориентировочно
ул. Ш.Валиханова
красная линия
граница земельного участка
6.50
4.54
136.00
136.20
135.50
136.60
137.30
136.23
136.30
136.17
1
136.20
136.20
136.00
136.30
137.30
136.20
136.80
136.30
136.80
137.30
2
3
136.20
135.90
135.84
136.06
136.40
136.30
136.60
136.57
136.40
136.80
6.50
8.80
24.08
6
7
8
9
10
11
5
136.23
136.44
136.48
135.76
136.32
137.08
136.54
137.09
136.71
136.56
136.52
135.89
135.77
136.02
135.58
135.52
135.47
135.63
135.50
135.62
135.57
135.88
135.83
135.74
135.96
135.58
135.52
135.52
135.88
135.91
135.84
135.52
135.78
136.10
136.28
136.40
136.50
136.54
136.63
136.31
136.34
136.29
136.30
136.31
136.63
136.49
136.52
136.53
136.36
136.32
136.63
136.62
136.63
136.52
136.53
136.36
136.32
136.63
136.62
136.63
136.52
136.53
136.36
136.32
136.63
136.62
136.63

				МНОГОКВАРТИРНЫЙ ЖИЛОЙ КОМПЛЕКС РАСПОЛОЖЕННЫЙ г. ПЕТРОПАВЛОВСК ул. Ш. Валиханова 9	Стадия	Лист	Листов
					ЭП	5	26
				ВИДОВАЯ КАРТИНКА	ТОО «LEVEX»		
Выполнил	Терехов А.		06.23				

				МНОГОКВАРТИРНЫЙ ЖИЛОЙ КОМПЛЕКС РАСПОЛОЖЕННЫЙ г. ПЕТРОПАВЛОВСК ул. Ш. Валиханова 9	Стадия	Лист	Листов
					ЭП	6	26
				ВИДОВАЯ КАРТИНКА	ТОО «LEVEX»		
Выполнил	Терехов А.		06.23				

				МНОГОКВАРТИРНЫЙ ЖИЛОЙ КОМПЛЕКС РАСПОЛОЖЕННЫЙ г. ПЕТРОПАВЛОВСК ул. Ш. Валиханова 9	Стадия	Лист	Листов
					ЭП	7	26
				ВИДОВАЯ КАРТИНКА	ТОО «LEVEX»		
Выполнил	Терехов А.		06.23				

				МНОГОКВАРТИРНЫЙ ЖИЛОЙ КОМПЛЕКС РАСПОЛОЖЕННЫЙ г. ПЕТРОПАВЛОВСК ул. Ш. Валиханова 9	Стадия	Лист	Листов
					ЭП	8	26
				ВИДОВАЯ КАРТИНКА	ТОО «LEVEX»		
Выполнил	Терехов А.		06.23				

				МНОГОКВАРТИРНЫЙ ЖИЛОЙ КОМПЛЕКС РАСПОЛОЖЕННЫЙ г. ПЕТРОПАВЛОВСК ул. Ш. Валиханова 9	Стадия	Лист	Листов
					ЭП	9	26
				НОЧНАЯ ПОДСВЕТКА	ТОО «LEVEX»		
Выполнил	Терехов А.		06.23				

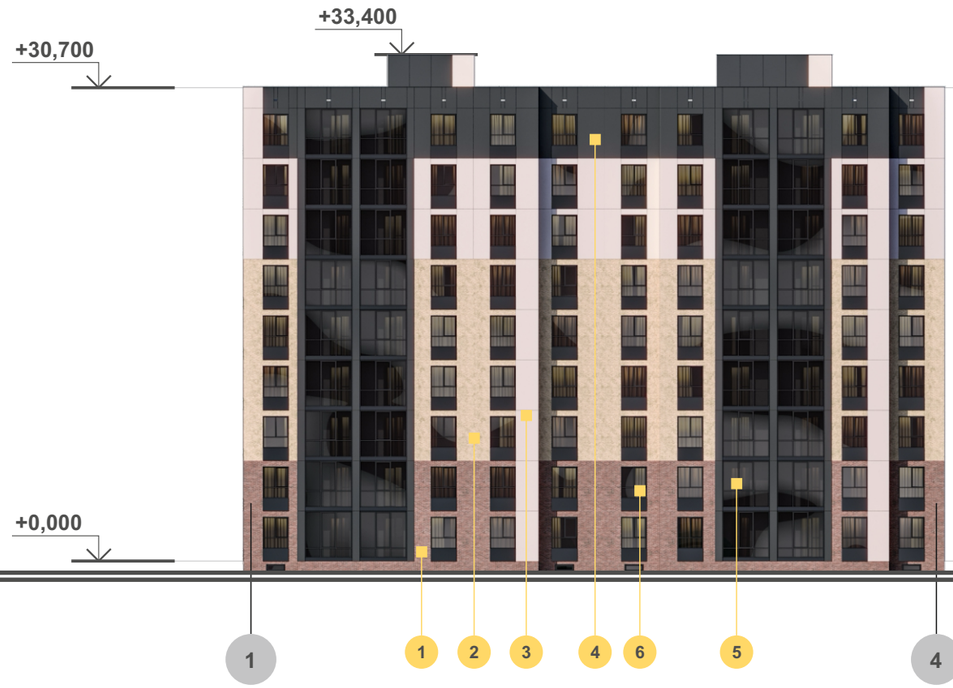

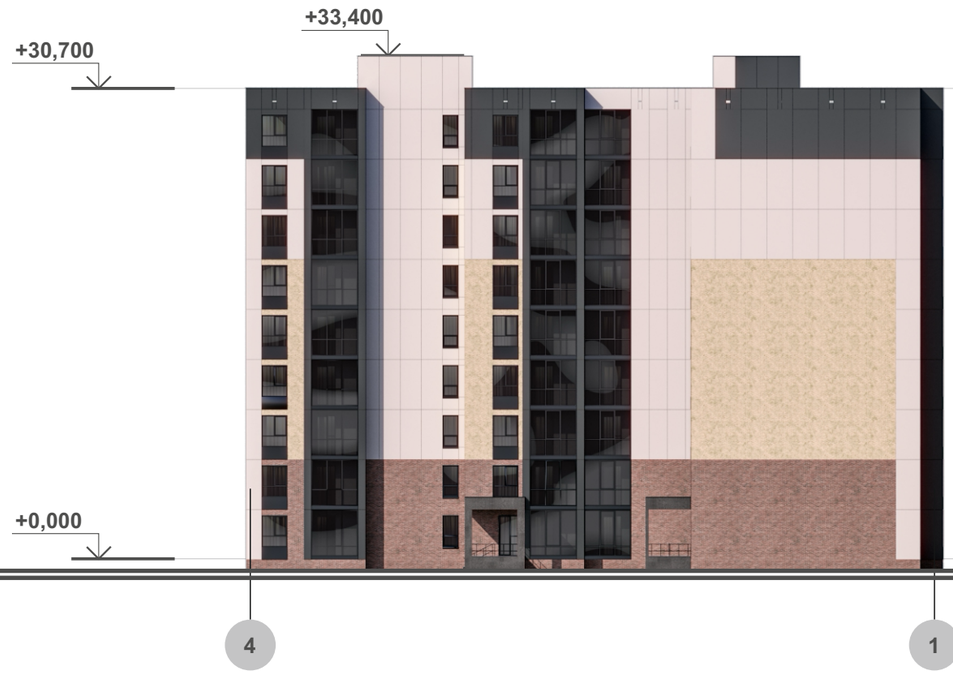

				МНОГОКВАРТИРНЫЙ ЖИЛОЙ КОМПЛЕКС РАСПОЛОЖЕННЫЙ г. ПЕТРОПАВЛОВСК ул. Ш. Валиханова 9	Стадия	Лист	Листов
					ЭП	10	26
				ФАСАДЫ В ОСЯХ 1-4;А-Г;4-1;Г-А	ТОО «LEVEX»		
Выполнил	Терехов А.		06.23				

№	Наименование	Тип отделки	Материал отделки	Эталон, № колера	Площадь, кв.м	Примечание
1	СТЕНА (ТИП 1)	ОТДЕЛКА	КЕРАМИЧЕСКИЙ КИРПИЧ	RAL2013	-	-
2	СТЕНА (ТИП 2)	ОТДЕЛКА	КЕРАМИЧЕСКИЙ КИРПИЧ	RAL1015	-	-
3	СТЕНА (ТИП 3)	ОТДЕЛКА	ПАНЕЛЬ HPL	RAL9010	-	-
4	СТЕНА (ТИП4)	ОТДЕЛКА	ПАНЕЛЬ HPL	RAL7015	-	-
5	ВИТРАЖ	ОСТЕКЛЕНИЕ	ТОНИРОВАННЫЙ СТЕКЛОБЛОК	ТОНИРОВАННЫЙ	-	-
		ИМПОСТ	АЛЮМИНИЕВЫЙ ИМПОСТ	RAL7024	-	-
6	ОКНА	ОСТЕКЛЕНИЕ	ПРОЗРАЧНЫЙ СТЕКЛОБЛОК	ПРОЗРАЧНЫЙ	-	-
		ИМПОСТ	ПЛАСТИКОВЫЙ ИМПОСТ	RAL7024	-	-
7	КРЫЛЬЦО	ОТДЕЛКА	ГРАНИТ	RAL 7039	-	-
					-	-
8					-	-
9					-	-

ЦВЕТ МАТЕРИАЛОВ НАРУЖНОЙ ОТДЕЛКИ ПРЕДСТАВИТЬ НА СОГЛАСОВАНИЕ.
ЦВЕТ МАТЕРИАЛОВ ПОДОБРАН В СООТВЕТСТВИИ С КАТАЛОГОМ ЦВЕТОВ «RAL-CLASSIC»

МАТЕРИАЛ ОТДЕЛКИ СОГЛАСОВАН С ЗАКАЗЧИКОМ:_____

				МНОГОКВАРТИРНЫЙ ЖИЛОЙ КОМПЛЕКС РАСПОЛОЖЕННЫЙ г. ПЕТРОПАВЛОВСК ул. Ш. Валиханова 9	Стадия	Лист	Листов
					ЭП	11	26
				ВЕДОМОСТЬ НАРУЖНЕЙ ОТДЕЛКИ	ТОО «LEVEX»		
Выполнил	Терехов А.		06.23				

СХЕМА БЛОКИРОВКИ

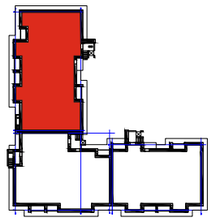

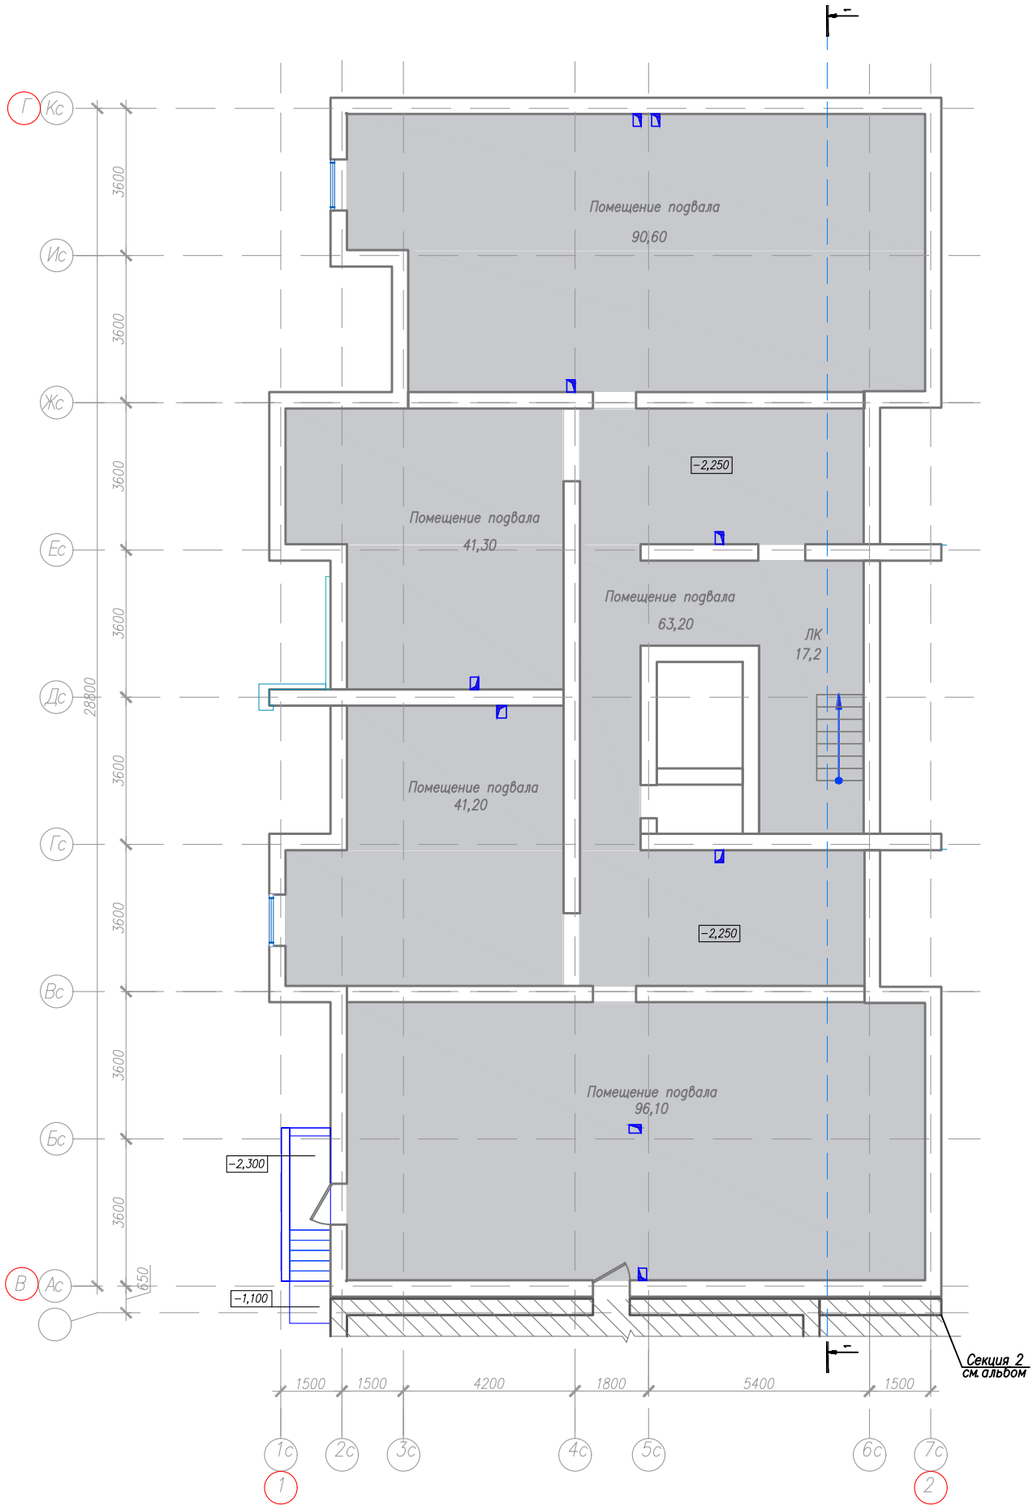

УСЛОВНЫЕ ОБОЗНАЧЕНИЯ

ПОМЕЩЕНИЯ ПОДВАЛА

				МНОГОКВАРТИРНЫЙ ЖИЛОЙ КОМПЛЕКС РАСПОЛОЖЕННЫЙ г. ПЕТРОПАВЛОВСК ул. Ш. Валиханова 9	Стадия	Лист	Листов
					ЭП	12	26
				СЕКЦИЯ 1 ПЛАН ПОДВАЛА	ТОО «LEVEX»		
Выполнил	Терехов А.		06.23				

СХЕМА БЛОКИРОВКИ

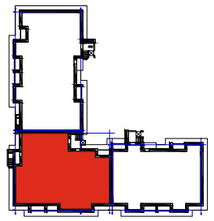

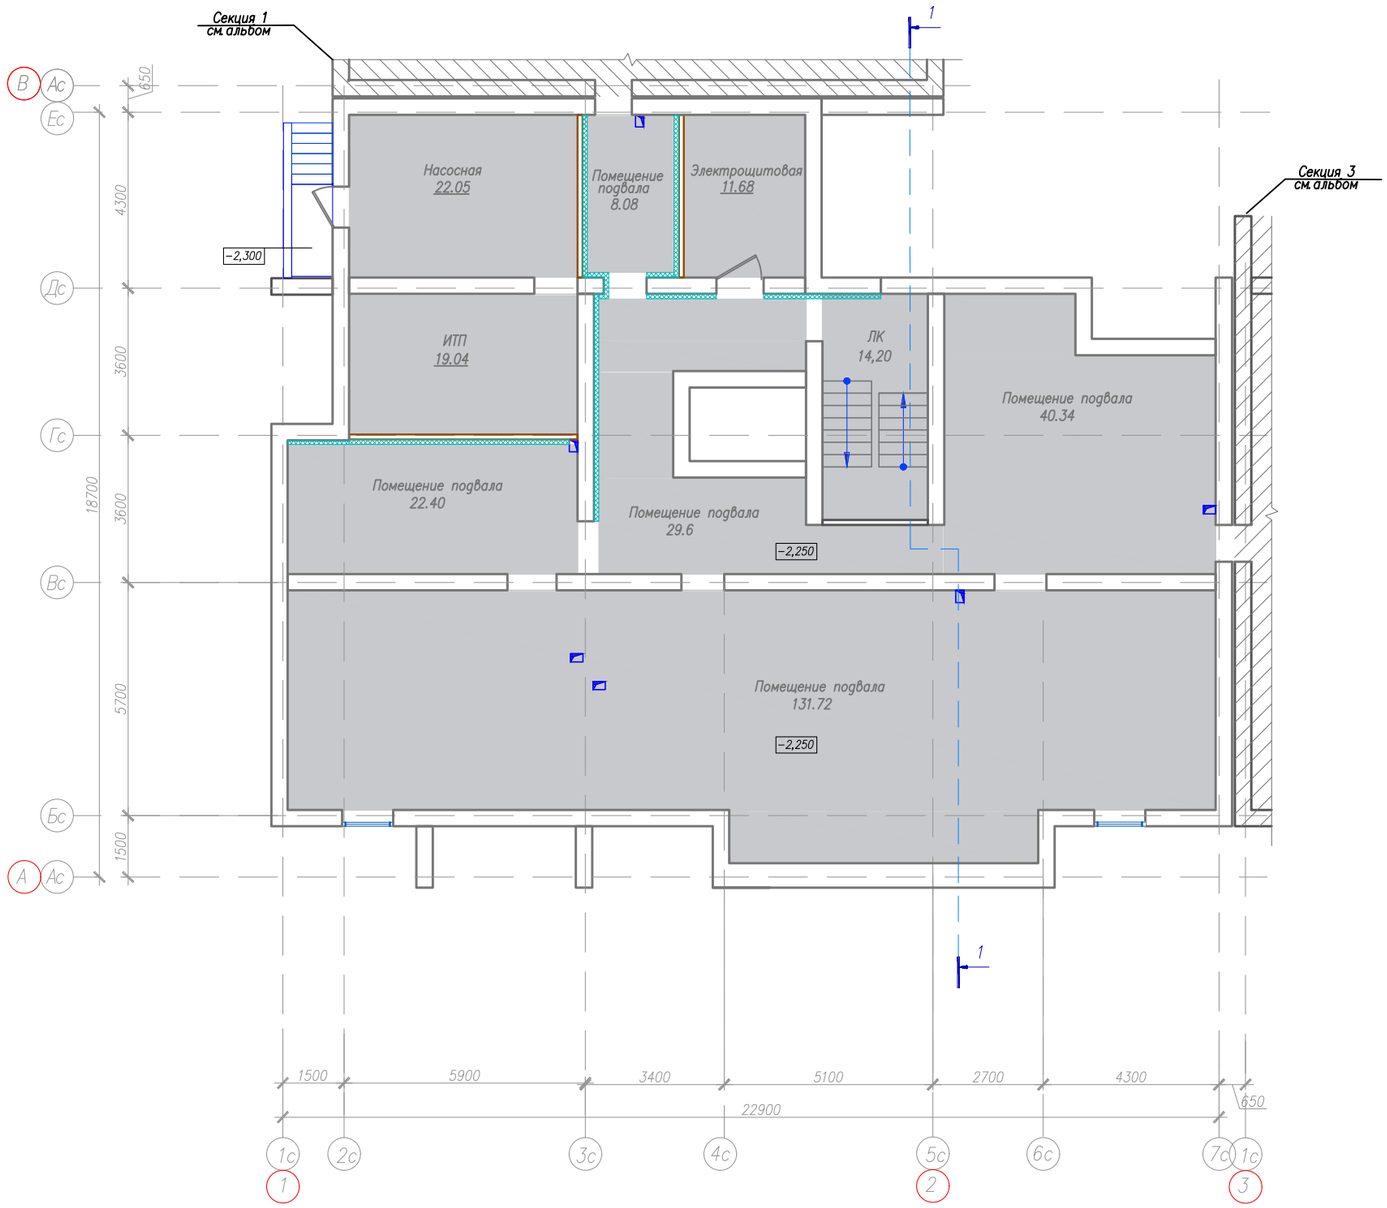

УСЛОВНЫЕ ОБОЗНАЧЕНИЯ

ПОМЕЩЕНИЯ ПОДВАЛА

				МНОГОКВАРТИРНЫЙ ЖИЛОЙ КОМПЛЕКС РАСПОЛОЖЕННЫЙ г. ПЕТРОПАВЛОВСК ул. Ш. Валиханова 9	Стадия	Лист	Листов
					ЭП	13	26
				СЕКЦИЯ 2 ПЛАН ПОДВАЛА	ТОО «LEVEX»		
Выполнил	Терехов А.		06.23				

СХЕМА БЛОКИРОВКИ

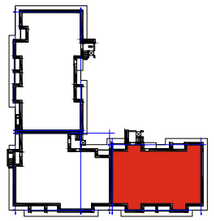

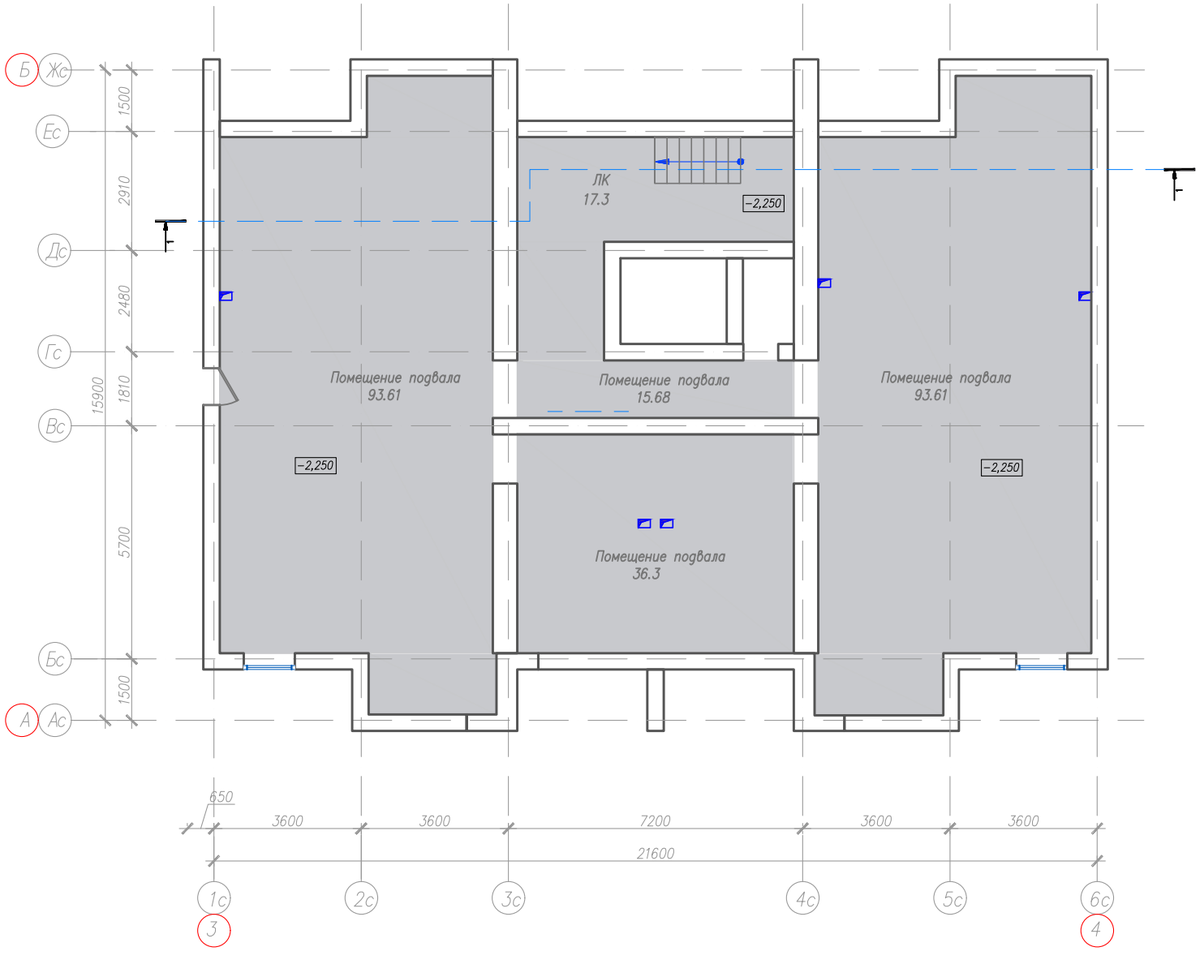

УСЛОВНЫЕ ОБОЗНАЧЕНИЯ

ПОМЕЩЕНИЯ ПОДВАЛА

				МНОГОКВАРТИРНЫЙ ЖИЛОЙ КОМПЛЕКС РАСПОЛОЖЕННЫЙ г. ПЕТРОПАВЛОВСК ул. Ш. Валиханова 9	Стадия	Лист	Листов
					ЭП	14	26
				СЕКЦИЯ 3 ПЛАН ПОДВАЛА	ТОО «LEVEX»		
Выполнил	Терехов А.		06.23				

СХЕМА БЛОКИРОВКИ

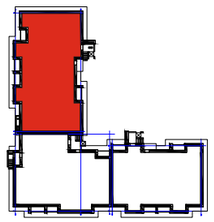

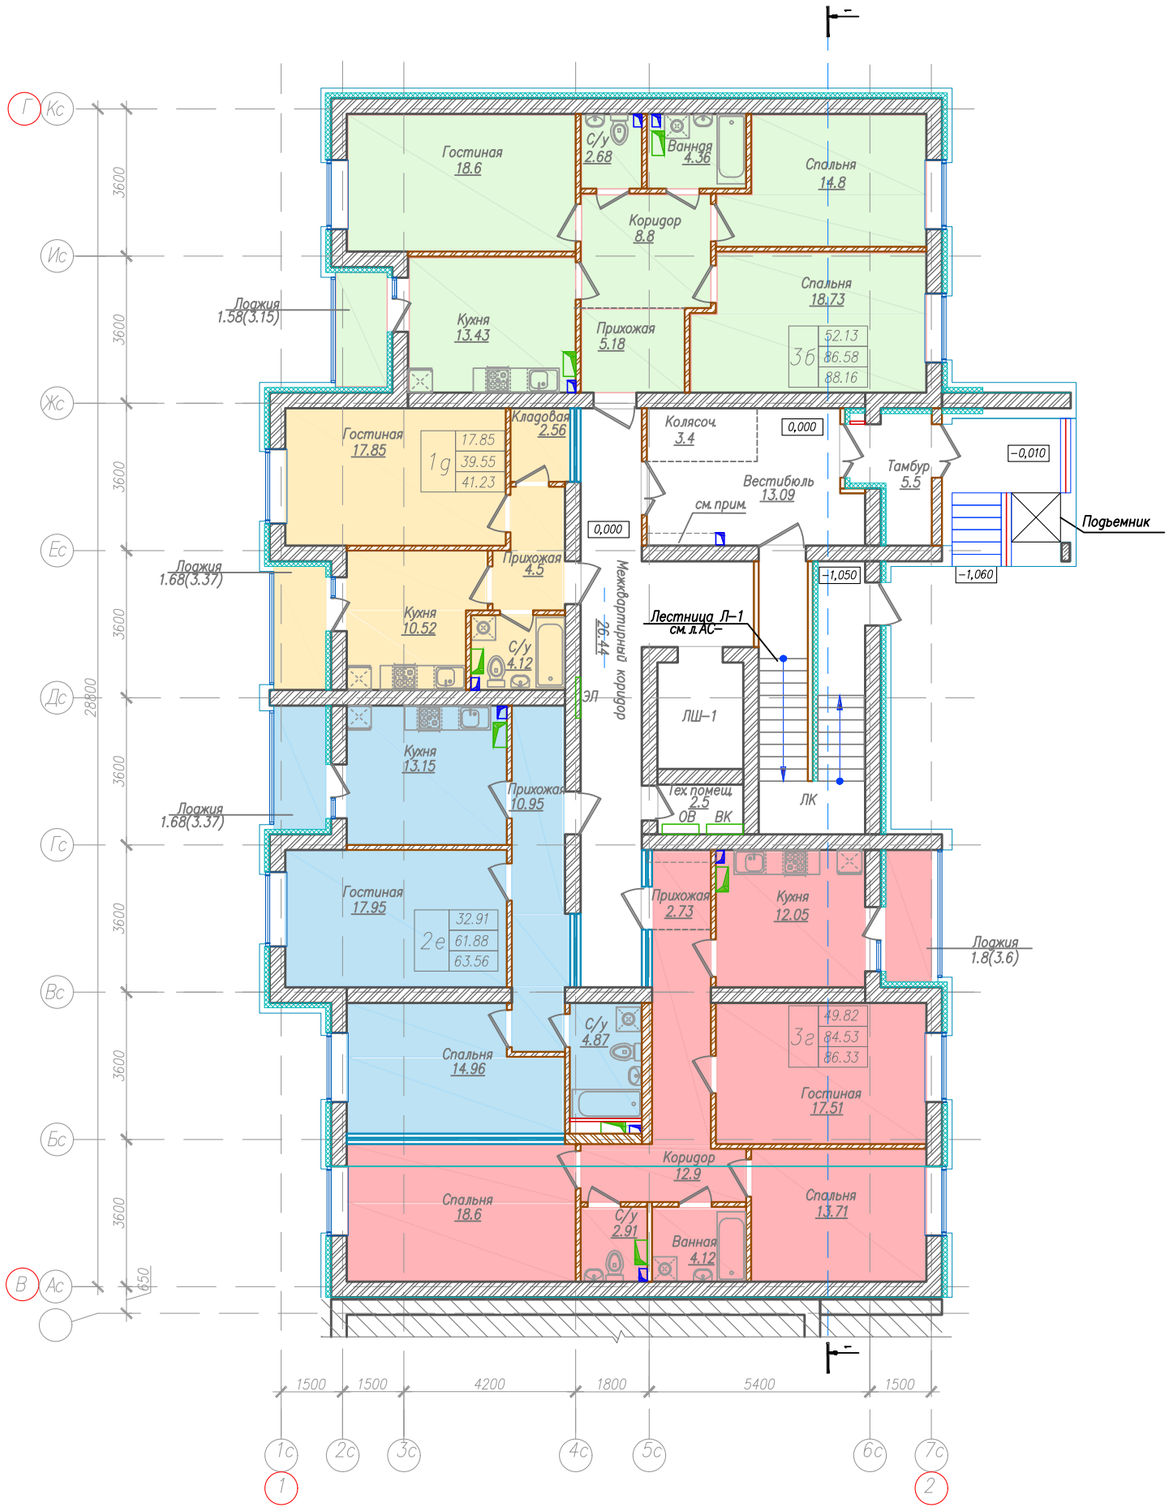

УСЛОВНЫЕ ОБОЗНАЧЕНИЯ

1 КОМНАТНЫЕ КВАРТИРЫ

2х КОМНАТНЫЕ КВАРТИРЫ

3х КОМНАТНЫЕ КВАРТИРЫ

				МНОГОКВАРТИРНЫЙ ЖИЛОЙ КОМПЛЕКС РАСПОЛОЖЕННЫЙ г. ПЕТРОПАВЛОВСК ул. Ш. Валиханова 9	Стадия	Лист	Листов
					ЭП	15	26
Выполнил	Терехов А.		06.23	СЕКЦИЯ 1 ПЛАН 1-ГО ЭТАЖА	ТОО «LEVEX»		

СХЕМА БЛОКИРОВКИ

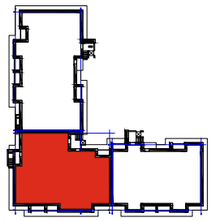

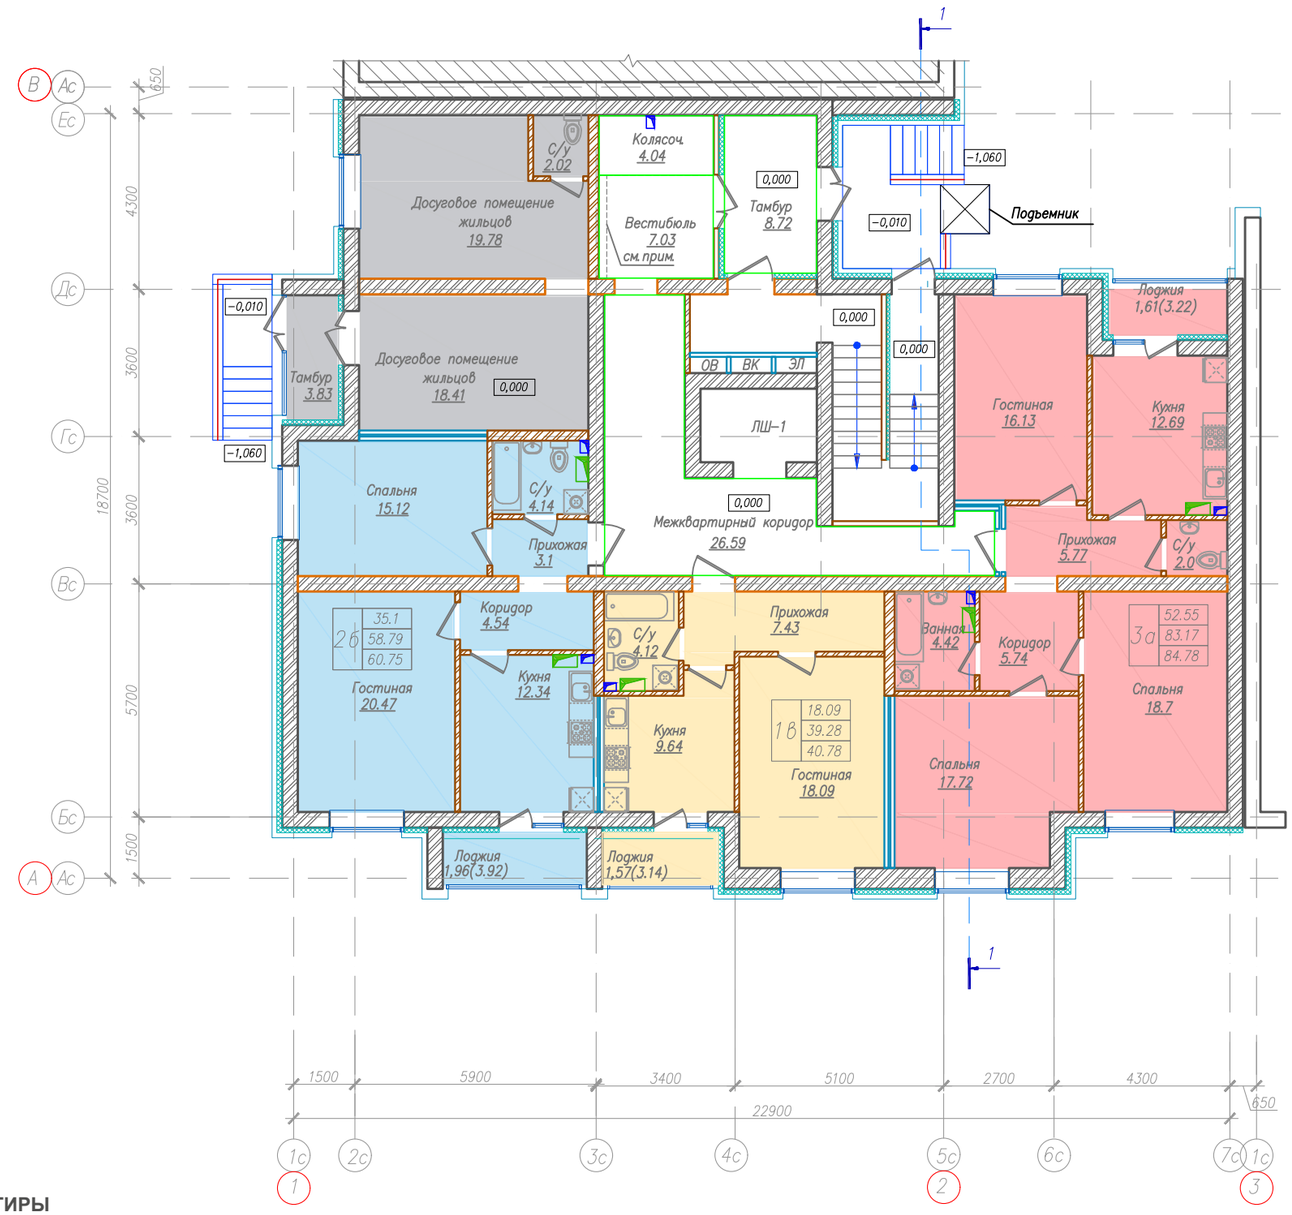

УСЛОВНЫЕ ОБОЗНАЧЕНИЯ

1 КОМНАТНЫЕ КВАРТИРЫ

2х КОМНАТНЫЕ КВАРТИРЫ

3х КОМНАТНЫЕ КВАРТИРЫ

				МНОГОКВАРТИРНЫЙ ЖИЛОЙ КОМПЛЕКС РАСПОЛОЖЕННЫЙ г. ПЕТРОПАВЛОВСК ул. Ш. Валиханова 9	Стадия	Лист	Листов
					ЭП	16	26
				СЕКЦИЯ 2 ПЛАН 1-ГО ЭТАЖА	ТОО «LEVEX»		
Выполнил	Терехов А.		06.23				

СХЕМА БЛОКИРОВКИ

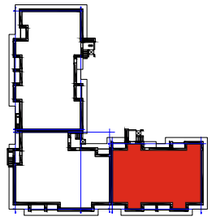

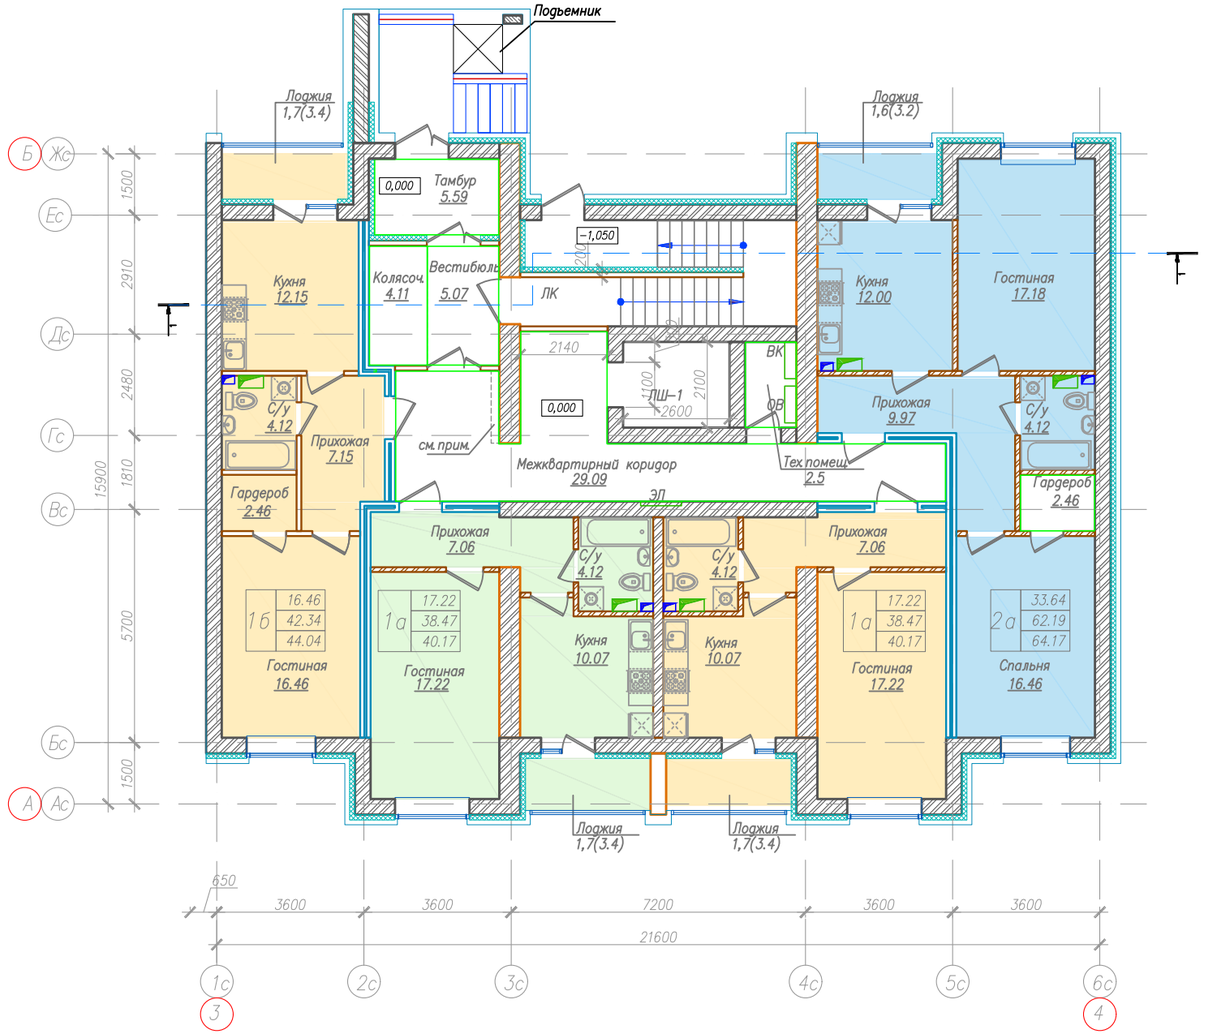

УСЛОВНЫЕ ОБОЗНАЧЕНИЯ

1 КОМНАТНЫЕ КВАРТИРЫ

2х КОМНАТНЫЕ КВАРТИРЫ

				МНОГОКВАРТИРНЫЙ ЖИЛОЙ КОМПЛЕКС РАСПОЛОЖЕННЫЙ г. ПЕТРОПАВЛОВСК ул. Ш. Валиханова 9	Стадия	Лист	Листов
					ЭП	17	26
				СЕКЦИЯ 3 ПЛАН 1-ГО ЭТАЖА	ТОО «LEVEX»		
Выполнил	Терехов А.		06.23				

СХЕМА БЛОКИРОВКИ

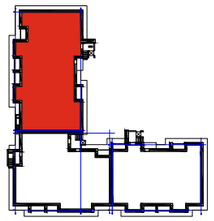

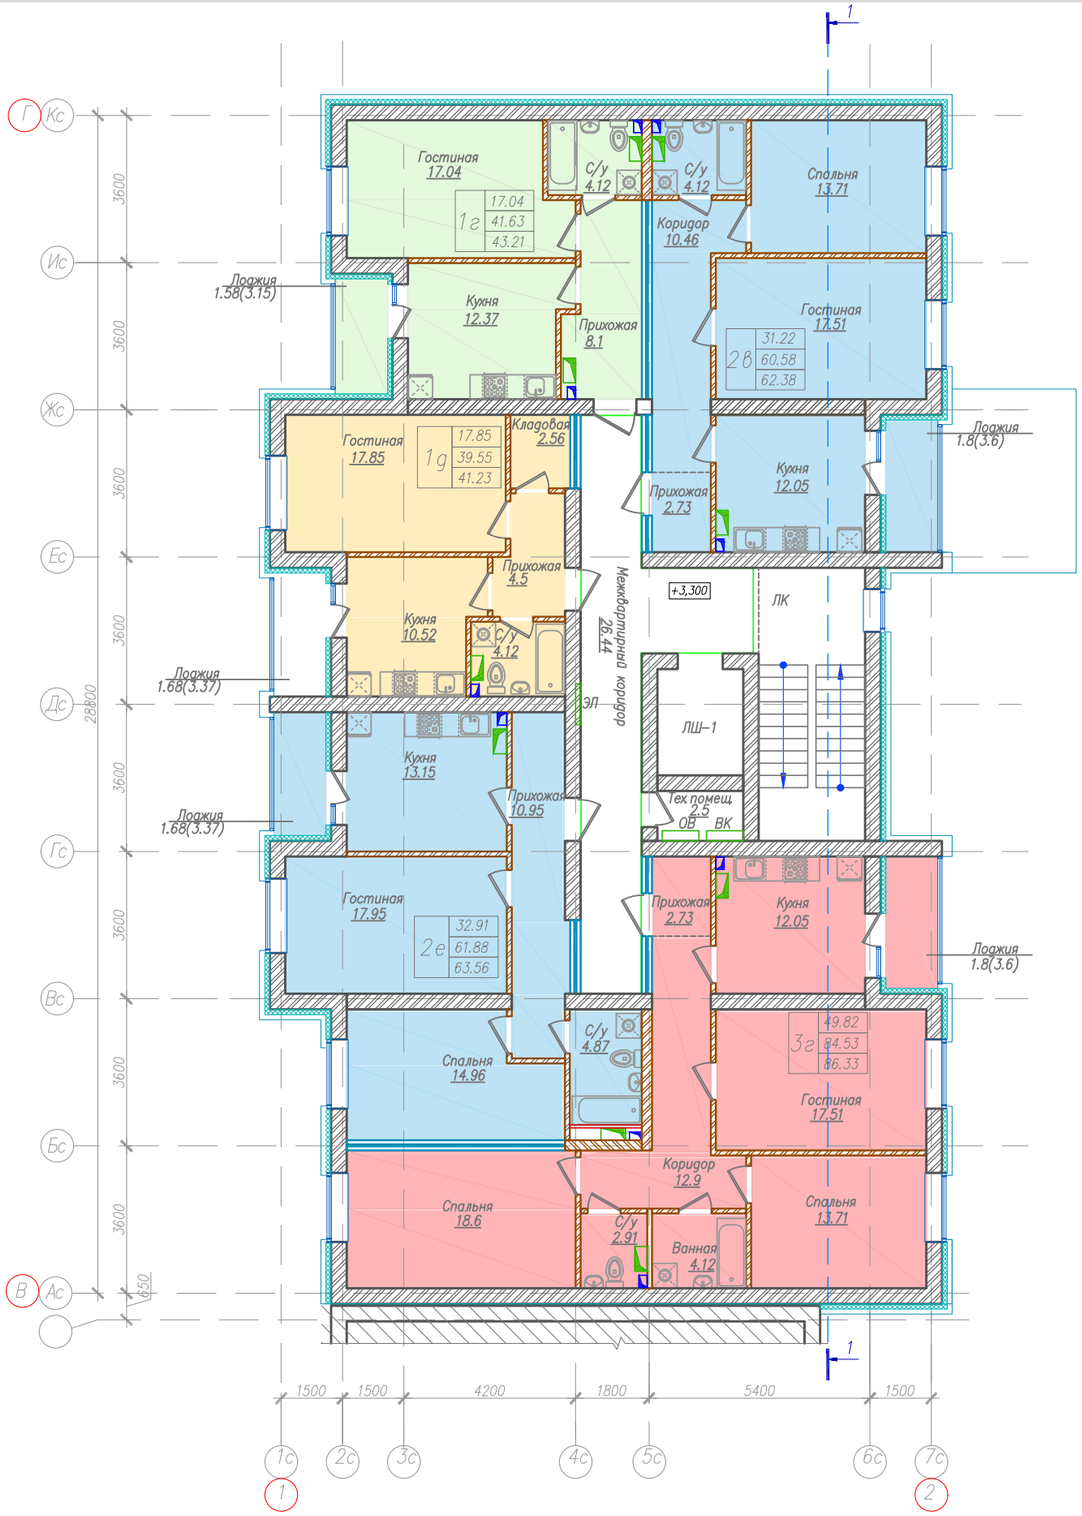

УСЛОВНЫЕ ОБОЗНАЧЕНИЯ

- 1 КОМНАТНЫЕ КВАРТИРЫ
- 2х КОМНАТНЫЕ КВАРТИРЫ
- 3х КОМНАТНЫЕ КВАРТИРЫ

				МНОГОКВАРТИРНЫЙ ЖИЛОЙ КОМПЛЕКС РАСПОЛОЖЕННЫЙ г. ПЕТРОПАВЛОВСК ул. Ш. Валиханова 9	Стадия	Лист	Листов
					ЭП	18	26
				СЕКЦИЯ 1. ПЛАН ТИПОВОГО ЭТАЖА	ТОО «LEVEX»		
Выполнил	Терехов А.		06.23				

СХЕМА БЛОКИРОВКИ

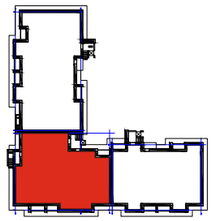

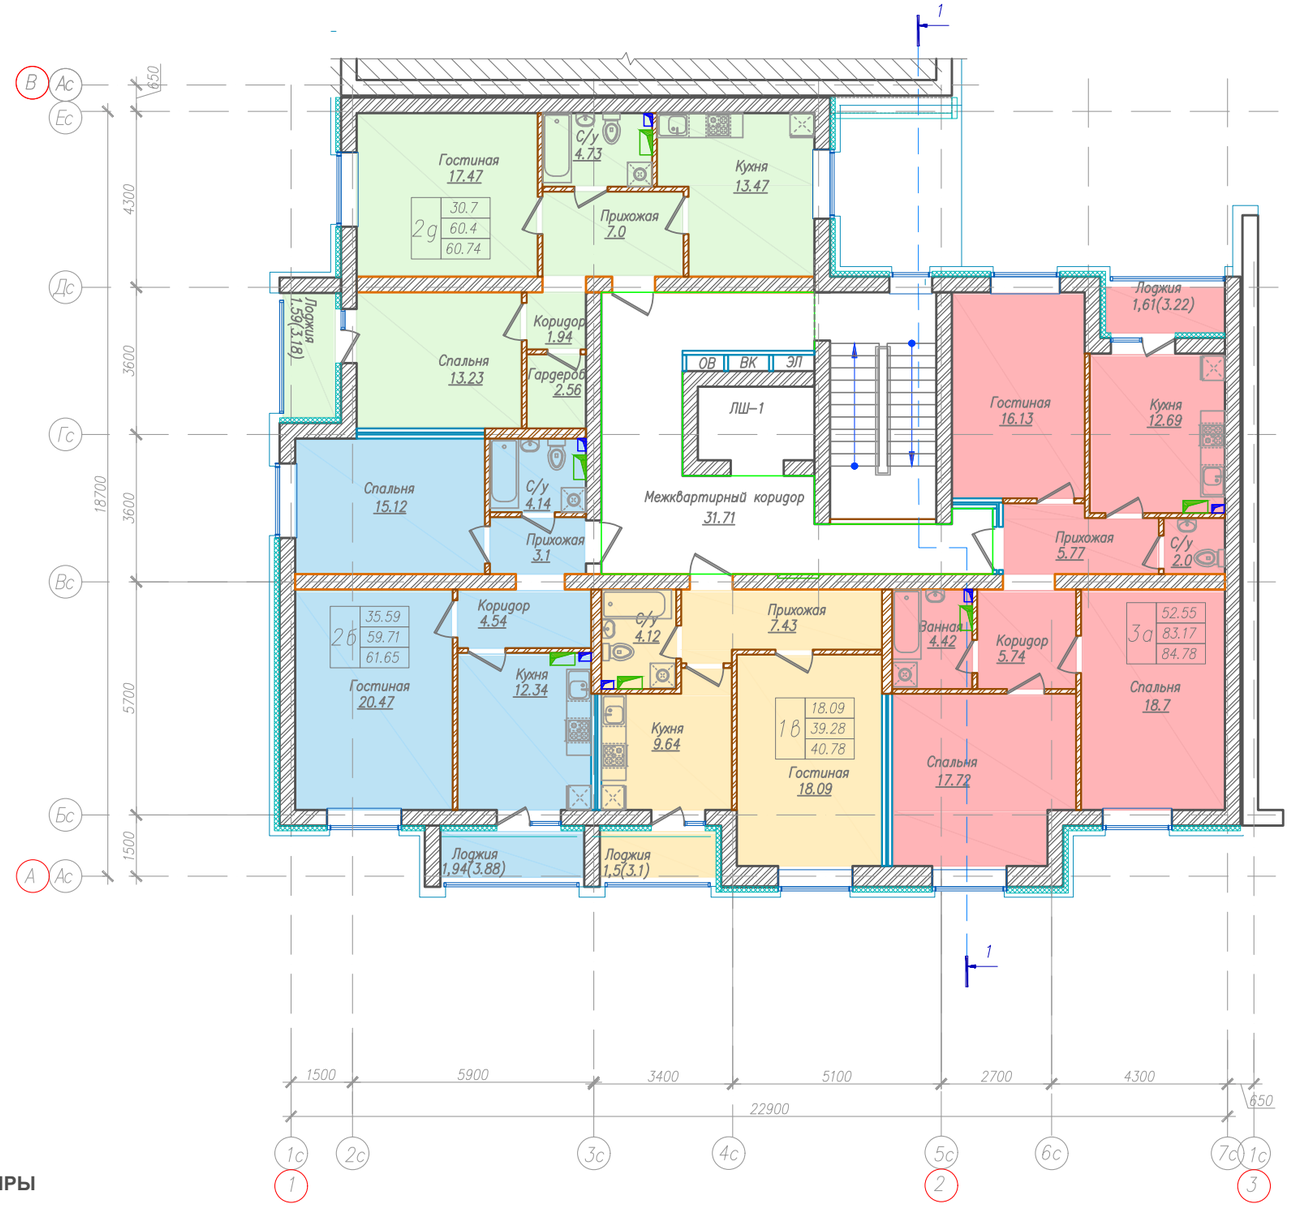

УСЛОВНЫЕ ОБОЗНАЧЕНИЯ

1 КОМНАТНЫЕ КВАРТИРЫ

2х КОМНАТНЫЕ КВАРТИРЫ

3х КОМНАТНЫЕ КВАРТИРЫ

				МНОГОКВАРТИРНЫЙ ЖИЛОЙ КОМПЛЕКС РАСПОЛОЖЕННЫЙ г. ПЕТРОПАВЛОВСК ул. Ш. Валиханова 9	Стадия	Лист	Листов
					ЭП	19	26
				СЕКЦИЯ 2. ПЛАН ТИПОВОГО ЭТАЖА	ТОО «LEVEX»		
Выполнил	Терехов А.		06.23				

СХЕМА БЛОКИРОВКИ

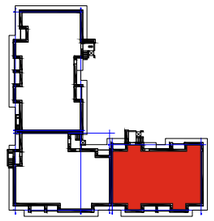

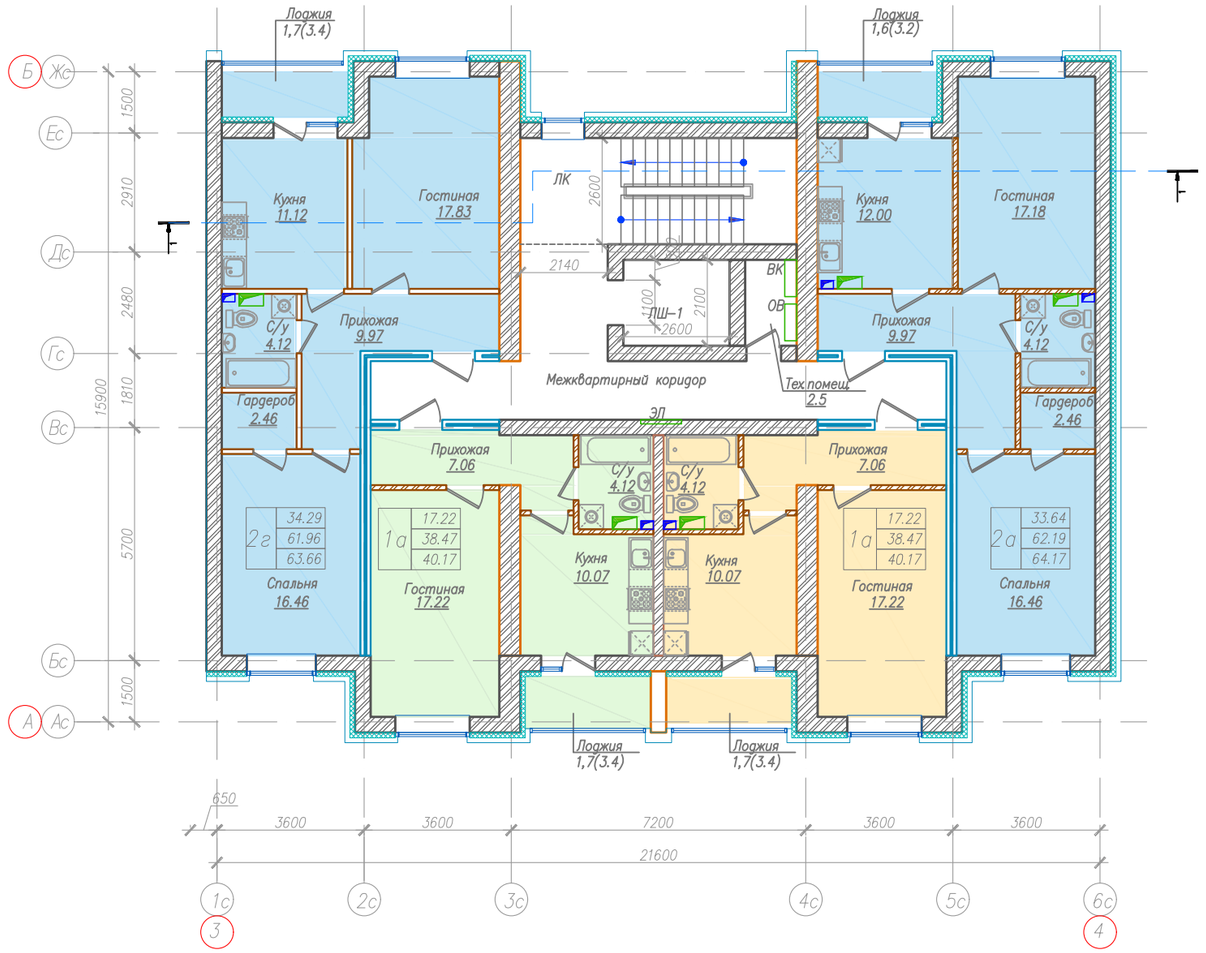

УСЛОВНЫЕ ОБОЗНАЧЕНИЯ

1 КОМНАТНЫЕ КВАРТИРЫ

2х КОМНАТНЫЕ КВАРТИРЫ

				МНОГОКВАРТИРНЫЙ ЖИЛОЙ КОМПЛЕКС РАСПОЛОЖЕННЫЙ г. ПЕТРОПАВЛОВСК ул. Ш. Валиханова 9	Стадия	Лист	Листов
					ЭП	20	26
				СЕКЦИЯ 3. ПЛАН ТИПОВОГО ЭТАЖА	ТОО «LEVEX»		
Выполнил	Терехов А.		06.23				

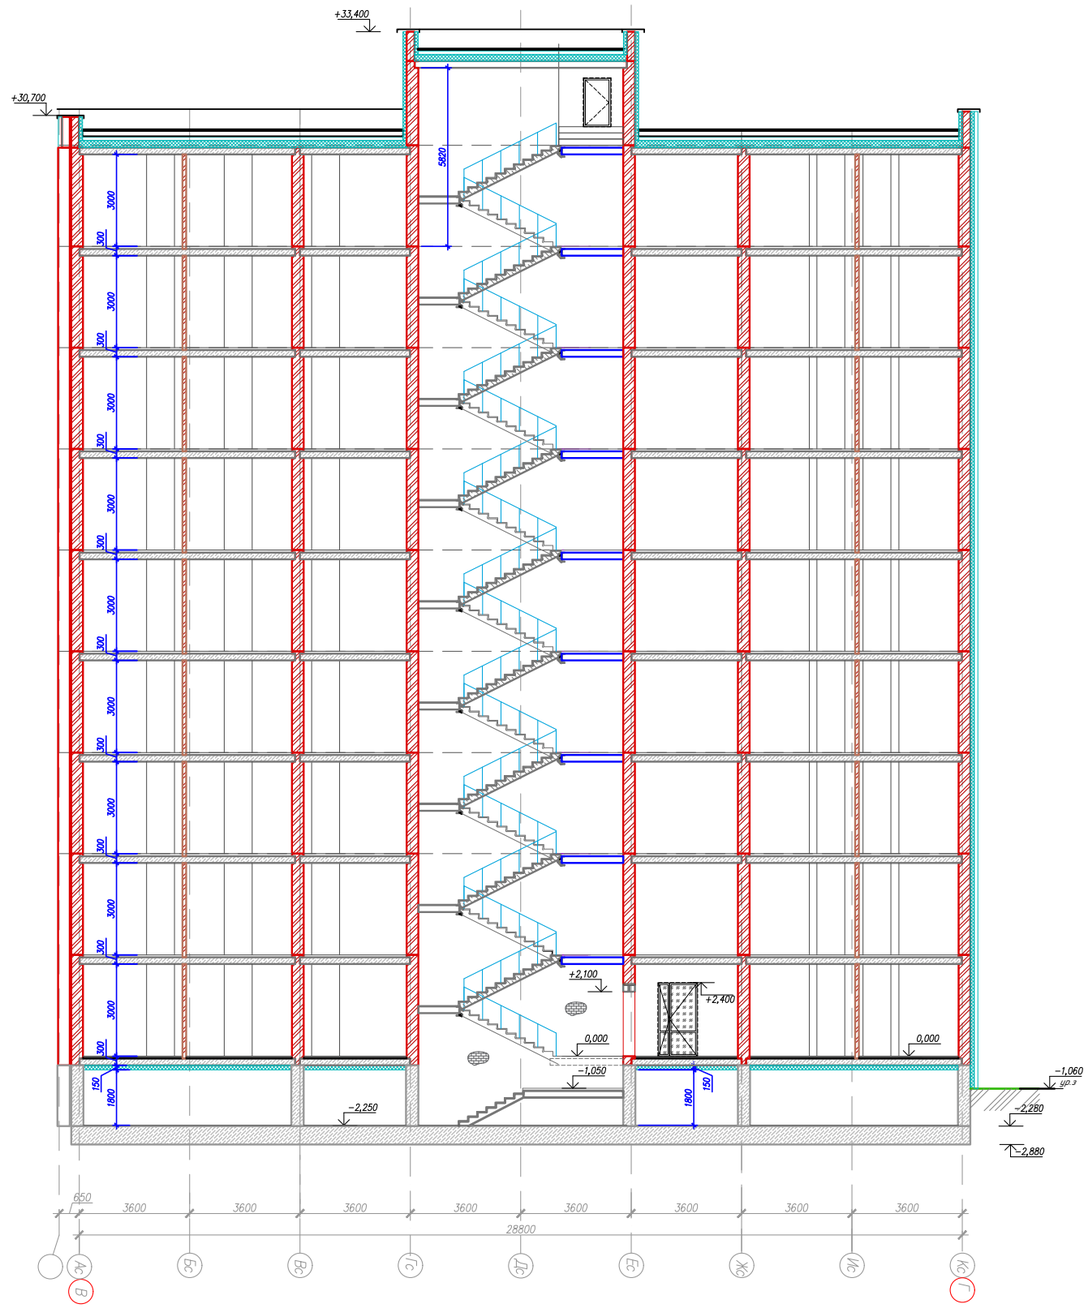

				МНОГОКВАРТИРНЫЙ ЖИЛОЙ КОМПЛЕКС РАСПОЛОЖЕННЫЙ г. ПЕТРОПАВЛОВСК ул. Ш. Валиханова 9	Стадия	Лист	Листов
					ЭП	21	26
				СЕКЦИЯ 1. РАЗРЕЗ 1-1	ТОО «LEVEX»		
Выполнил	Терехов А.		06.23				

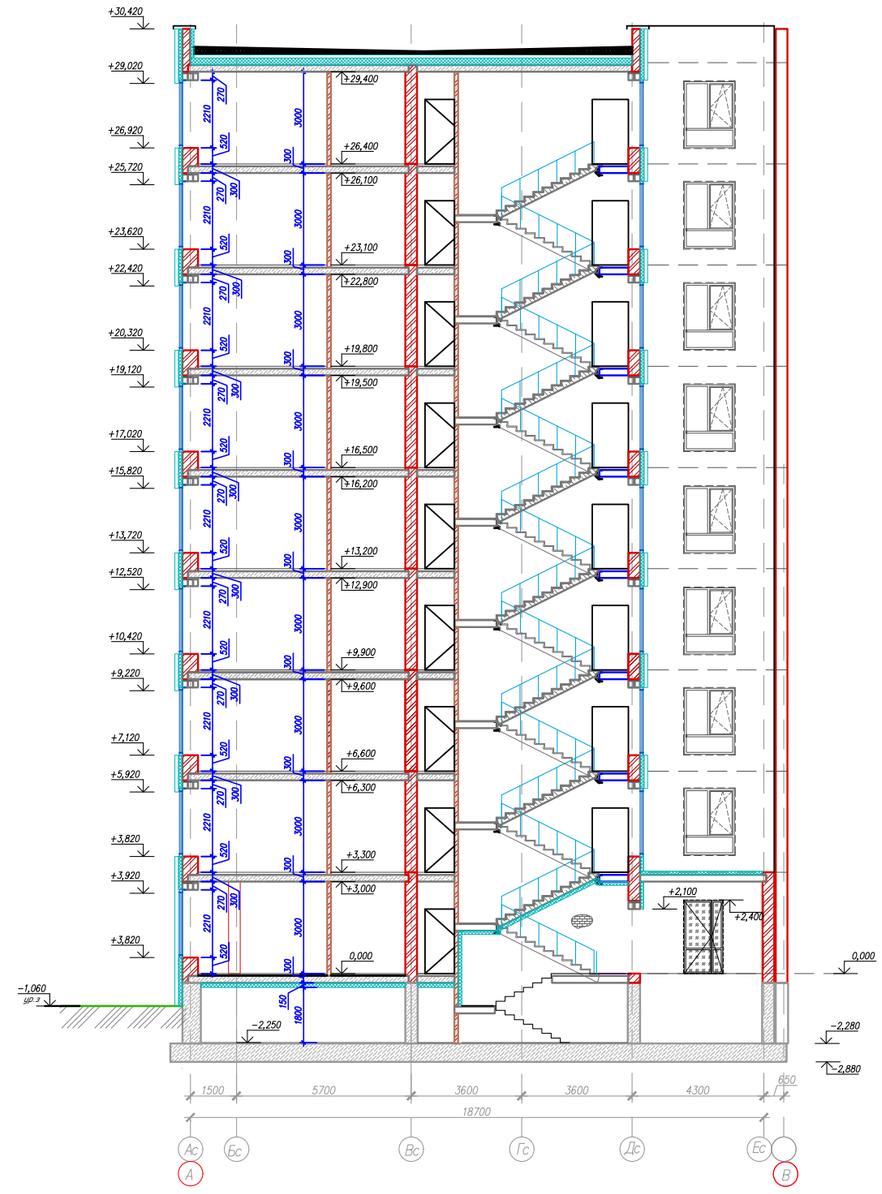

				МНОГОКВАРТИРНЫЙ ЖИЛОЙ КОМПЛЕКС РАСПОЛОЖЕННЫЙ г. ПЕТРОПАВЛОВСК ул. Ш. Валиханова 9	Стадия	Лист	Листов
					ЭП	22	26
				СЕКЦИЯ 2 РАЗРЕЗ 1-1	ТОО «LEVEX»		
Выполнил	Терехов А.		06.23				

СХЕМА БЛОКИРОВКИ

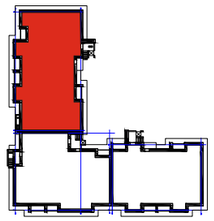

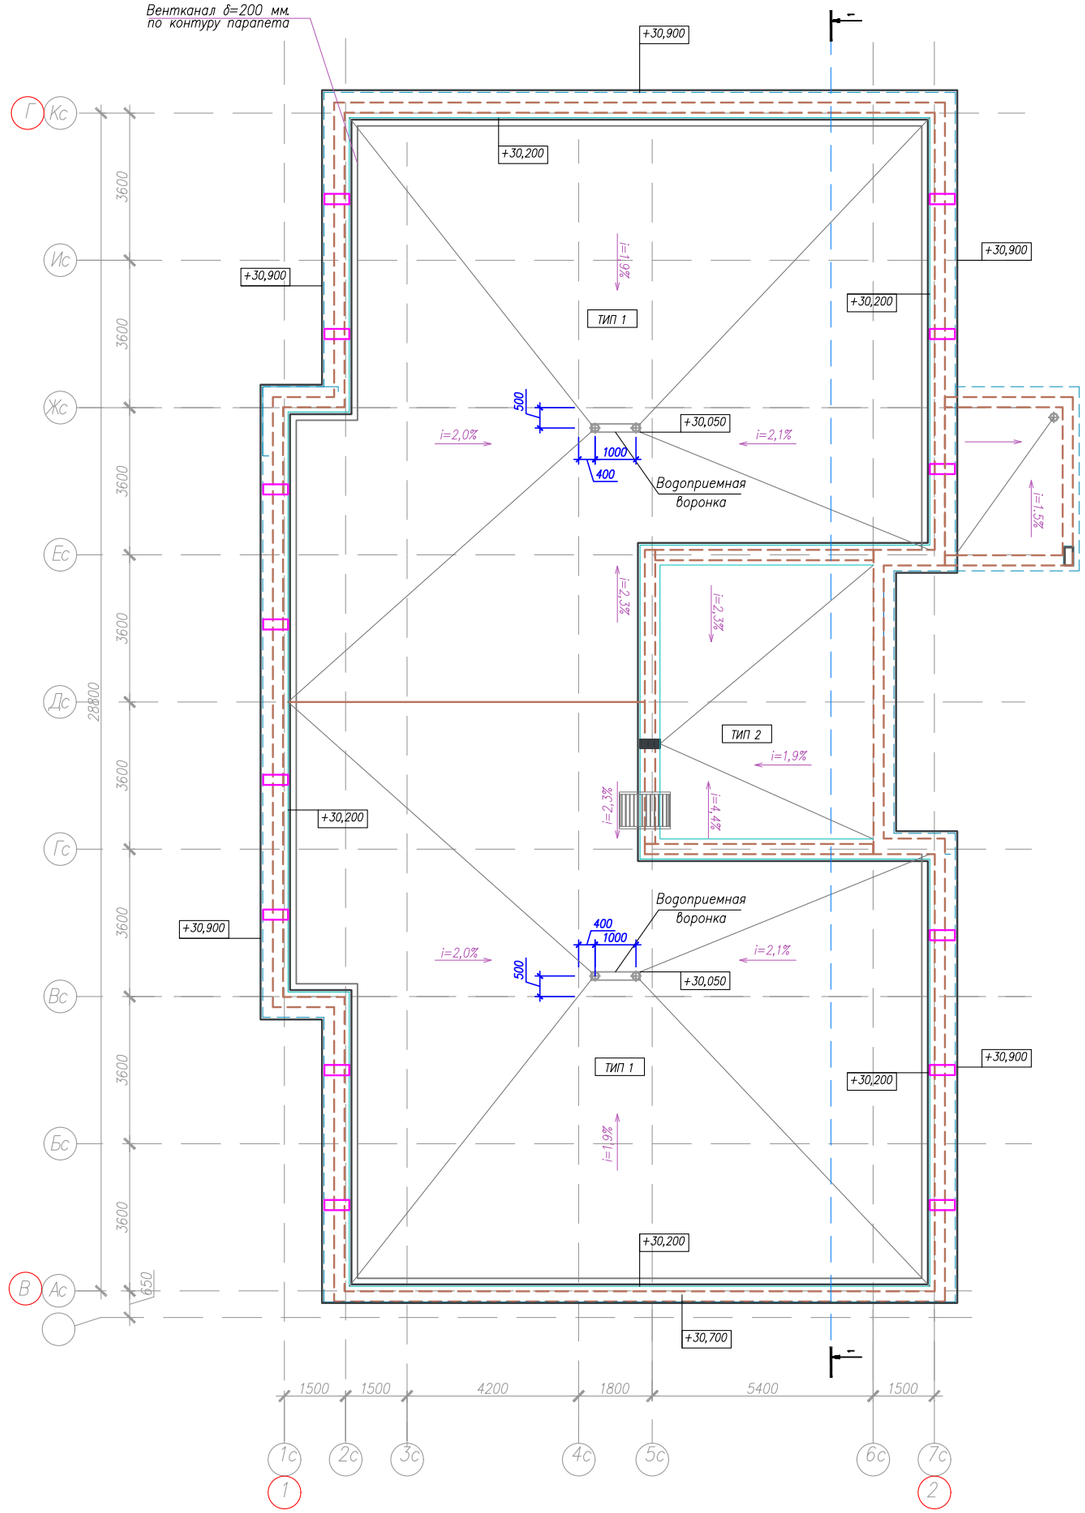

				МНОГОКВАРТИРНЫЙ ЖИЛОЙ КОМПЛЕКС РАСПОЛОЖЕННЫЙ г. ПЕТРОПАВЛОВСК ул. Ш. Валиханова 9	Стадия	Лист	Листов
					ЭП	23	26
				СЕКЦИЯ 1. ПЛАН КРОВЛИ	ТОО «LEVEX»		
Выполнил	Терехов А.		06.23				

СХЕМА БЛОКИРОВКИ

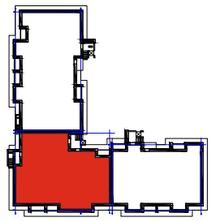

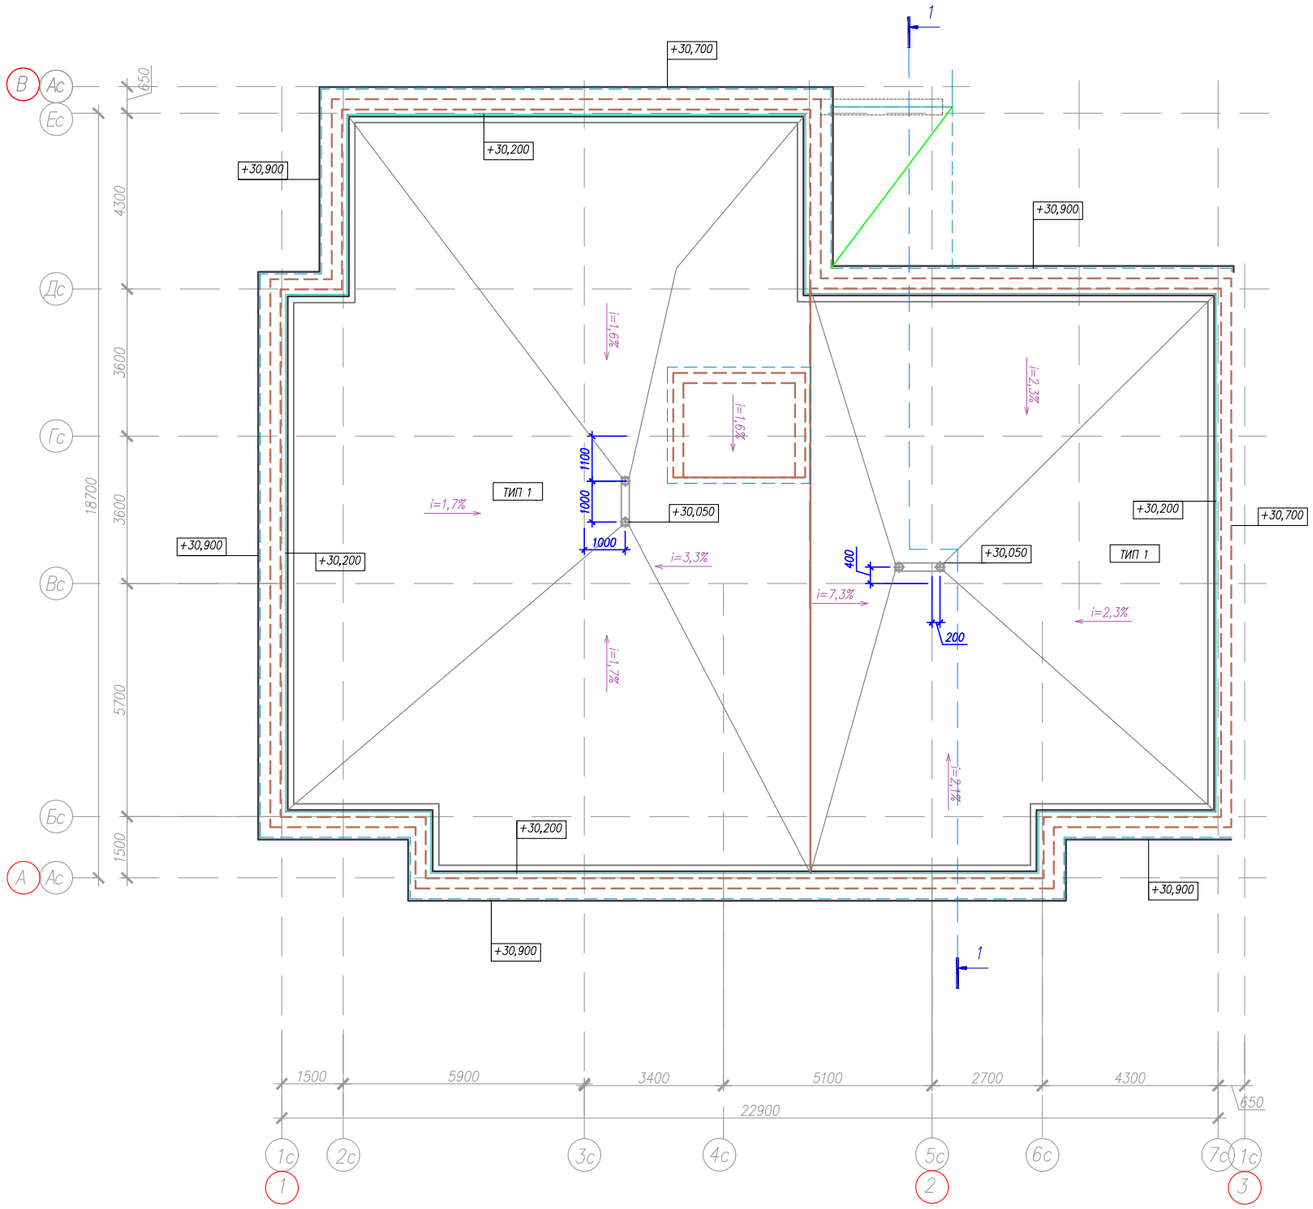

				МНОГОКВАРТИРНЫЙ ЖИЛОЙ КОМПЛЕКС РАСПОЛОЖЕННЫЙ г. ПЕТРОПАВЛОВСК ул. Ш. Валиханова 9	Стадия	Лист	Листов
					ЭП	24	26
				СЕКЦИЯ 2. ПЛАН КРОВЛИ	ТОО «LEVEX»		
Выполнил	Терехов А.		06.23				

СХЕМА БЛОКИРОВКИ

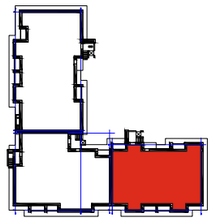

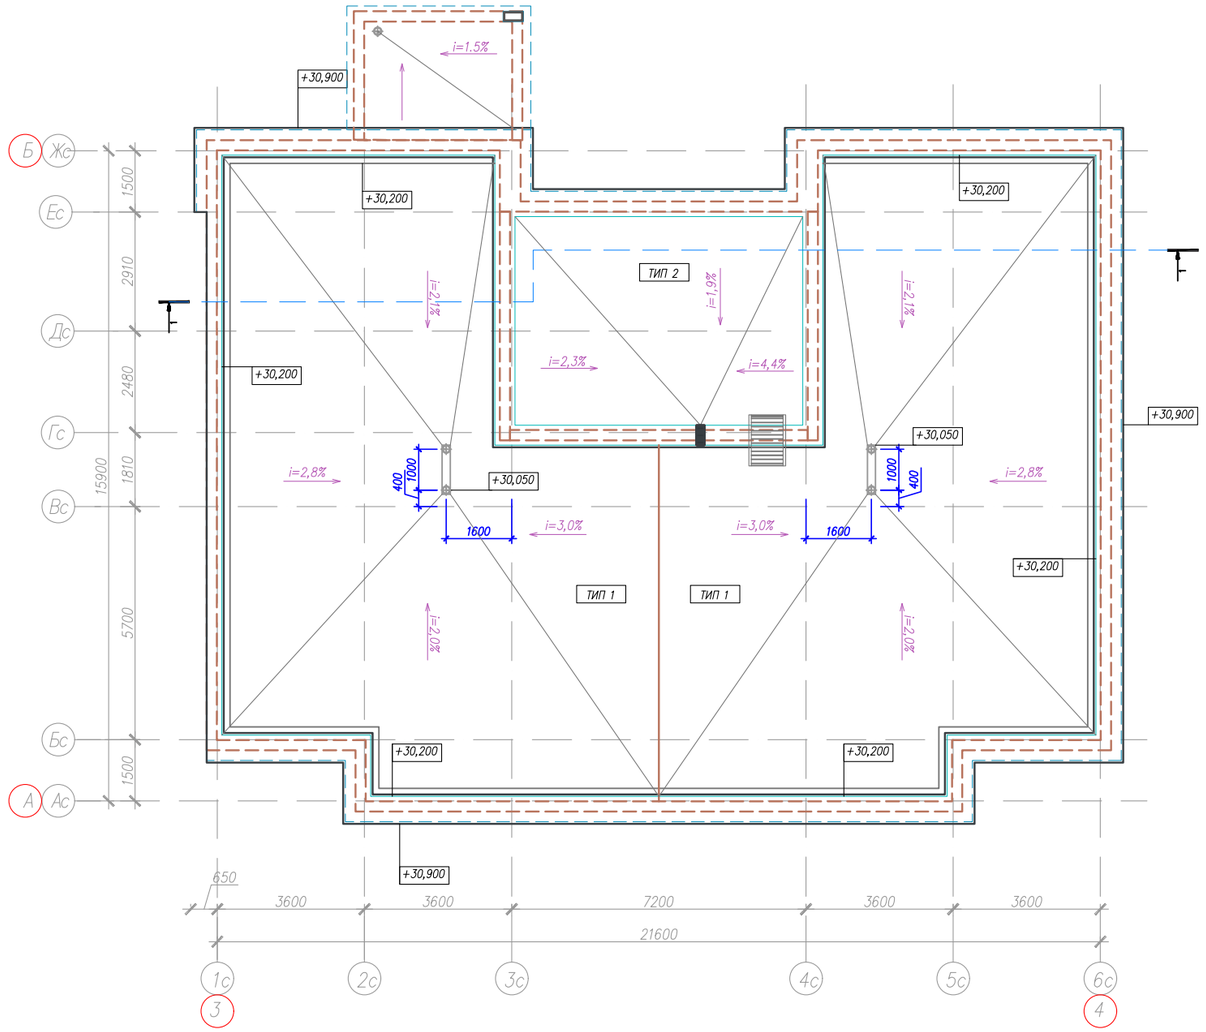

				МНОГОКВАРТИРНЫЙ ЖИЛОЙ КОМПЛЕКС РАСПОЛОЖЕННЫЙ г. ПЕТРОПАВЛОВСК ул. Ш. Валиханова 9	Стадия	Лист	Листов
					ЭП	25	26
				СЕКЦИЯ 3. ПЛАН КРОВЛИ	ТОО «LEVEX»		
Выполнил	Терехов А.		06.23				

	Урна (9001)		Игровой модуль Домик (5005)		Игровой модуль Кораблик (6102)	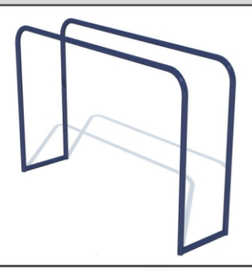	Брусья паралельные (7921)
	Скамейка (8004)		Игровой модуль Горка жираф (5206)	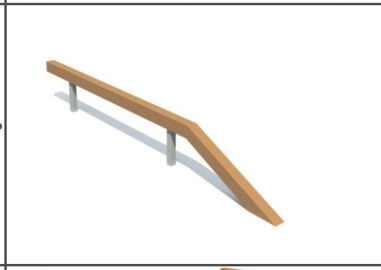	Спортивное оборудование (7820)	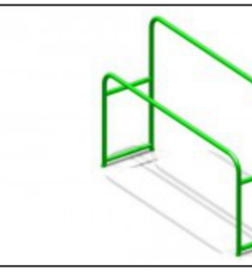	Брусья разновысокие (7922)
	Скамейка (8002)	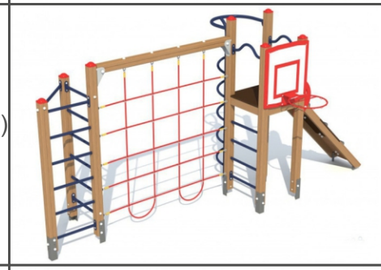	Спортивный комплекс (7822)		Спортивный комплекс (7824)		Вазон Кадка 85
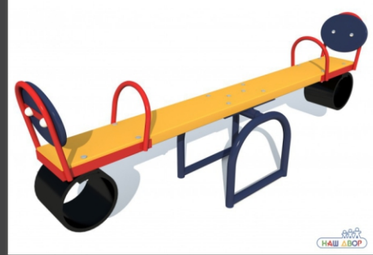	Качель - балансир (6201)		Карусель штурвал (6505)		Спортивное оборудование (7910)		-
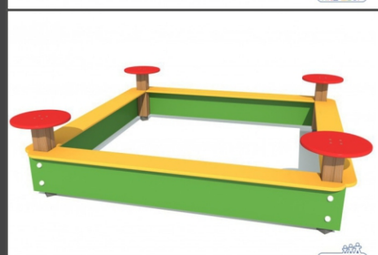	Игровой модуль Песочница (5305)	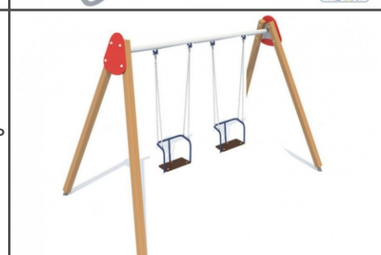	Качели двухпролетные (6314)	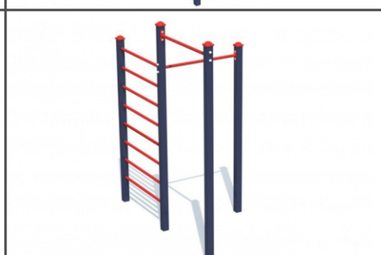	Спортивное оборудование (7910)		-

МАЛЫЕ АРХИТЕКТУРНЫЕ ФОРМЫ СОГЛАСОВАНЫ С ЗАКАЗЧИКОМ:_____

				МНОГОКВАРТИРНЫЙ ЖИЛОЙ КОМПЛЕКС РАСПОЛОЖЕННЫЙ г. ПЕТРОПАВЛОВСК ул. Ш. Валиханова 9	Стадия	Лист	Листов
					ЭП	26	26
				МАЛЫЕ АРХИТЕКТУРНЫЕ ФОРМЫ	ТОО «LEVEX»		
Выполнил	Терехов А.		06.23				